



# PLANTA DESAGÜES SOTANO

1 : 100

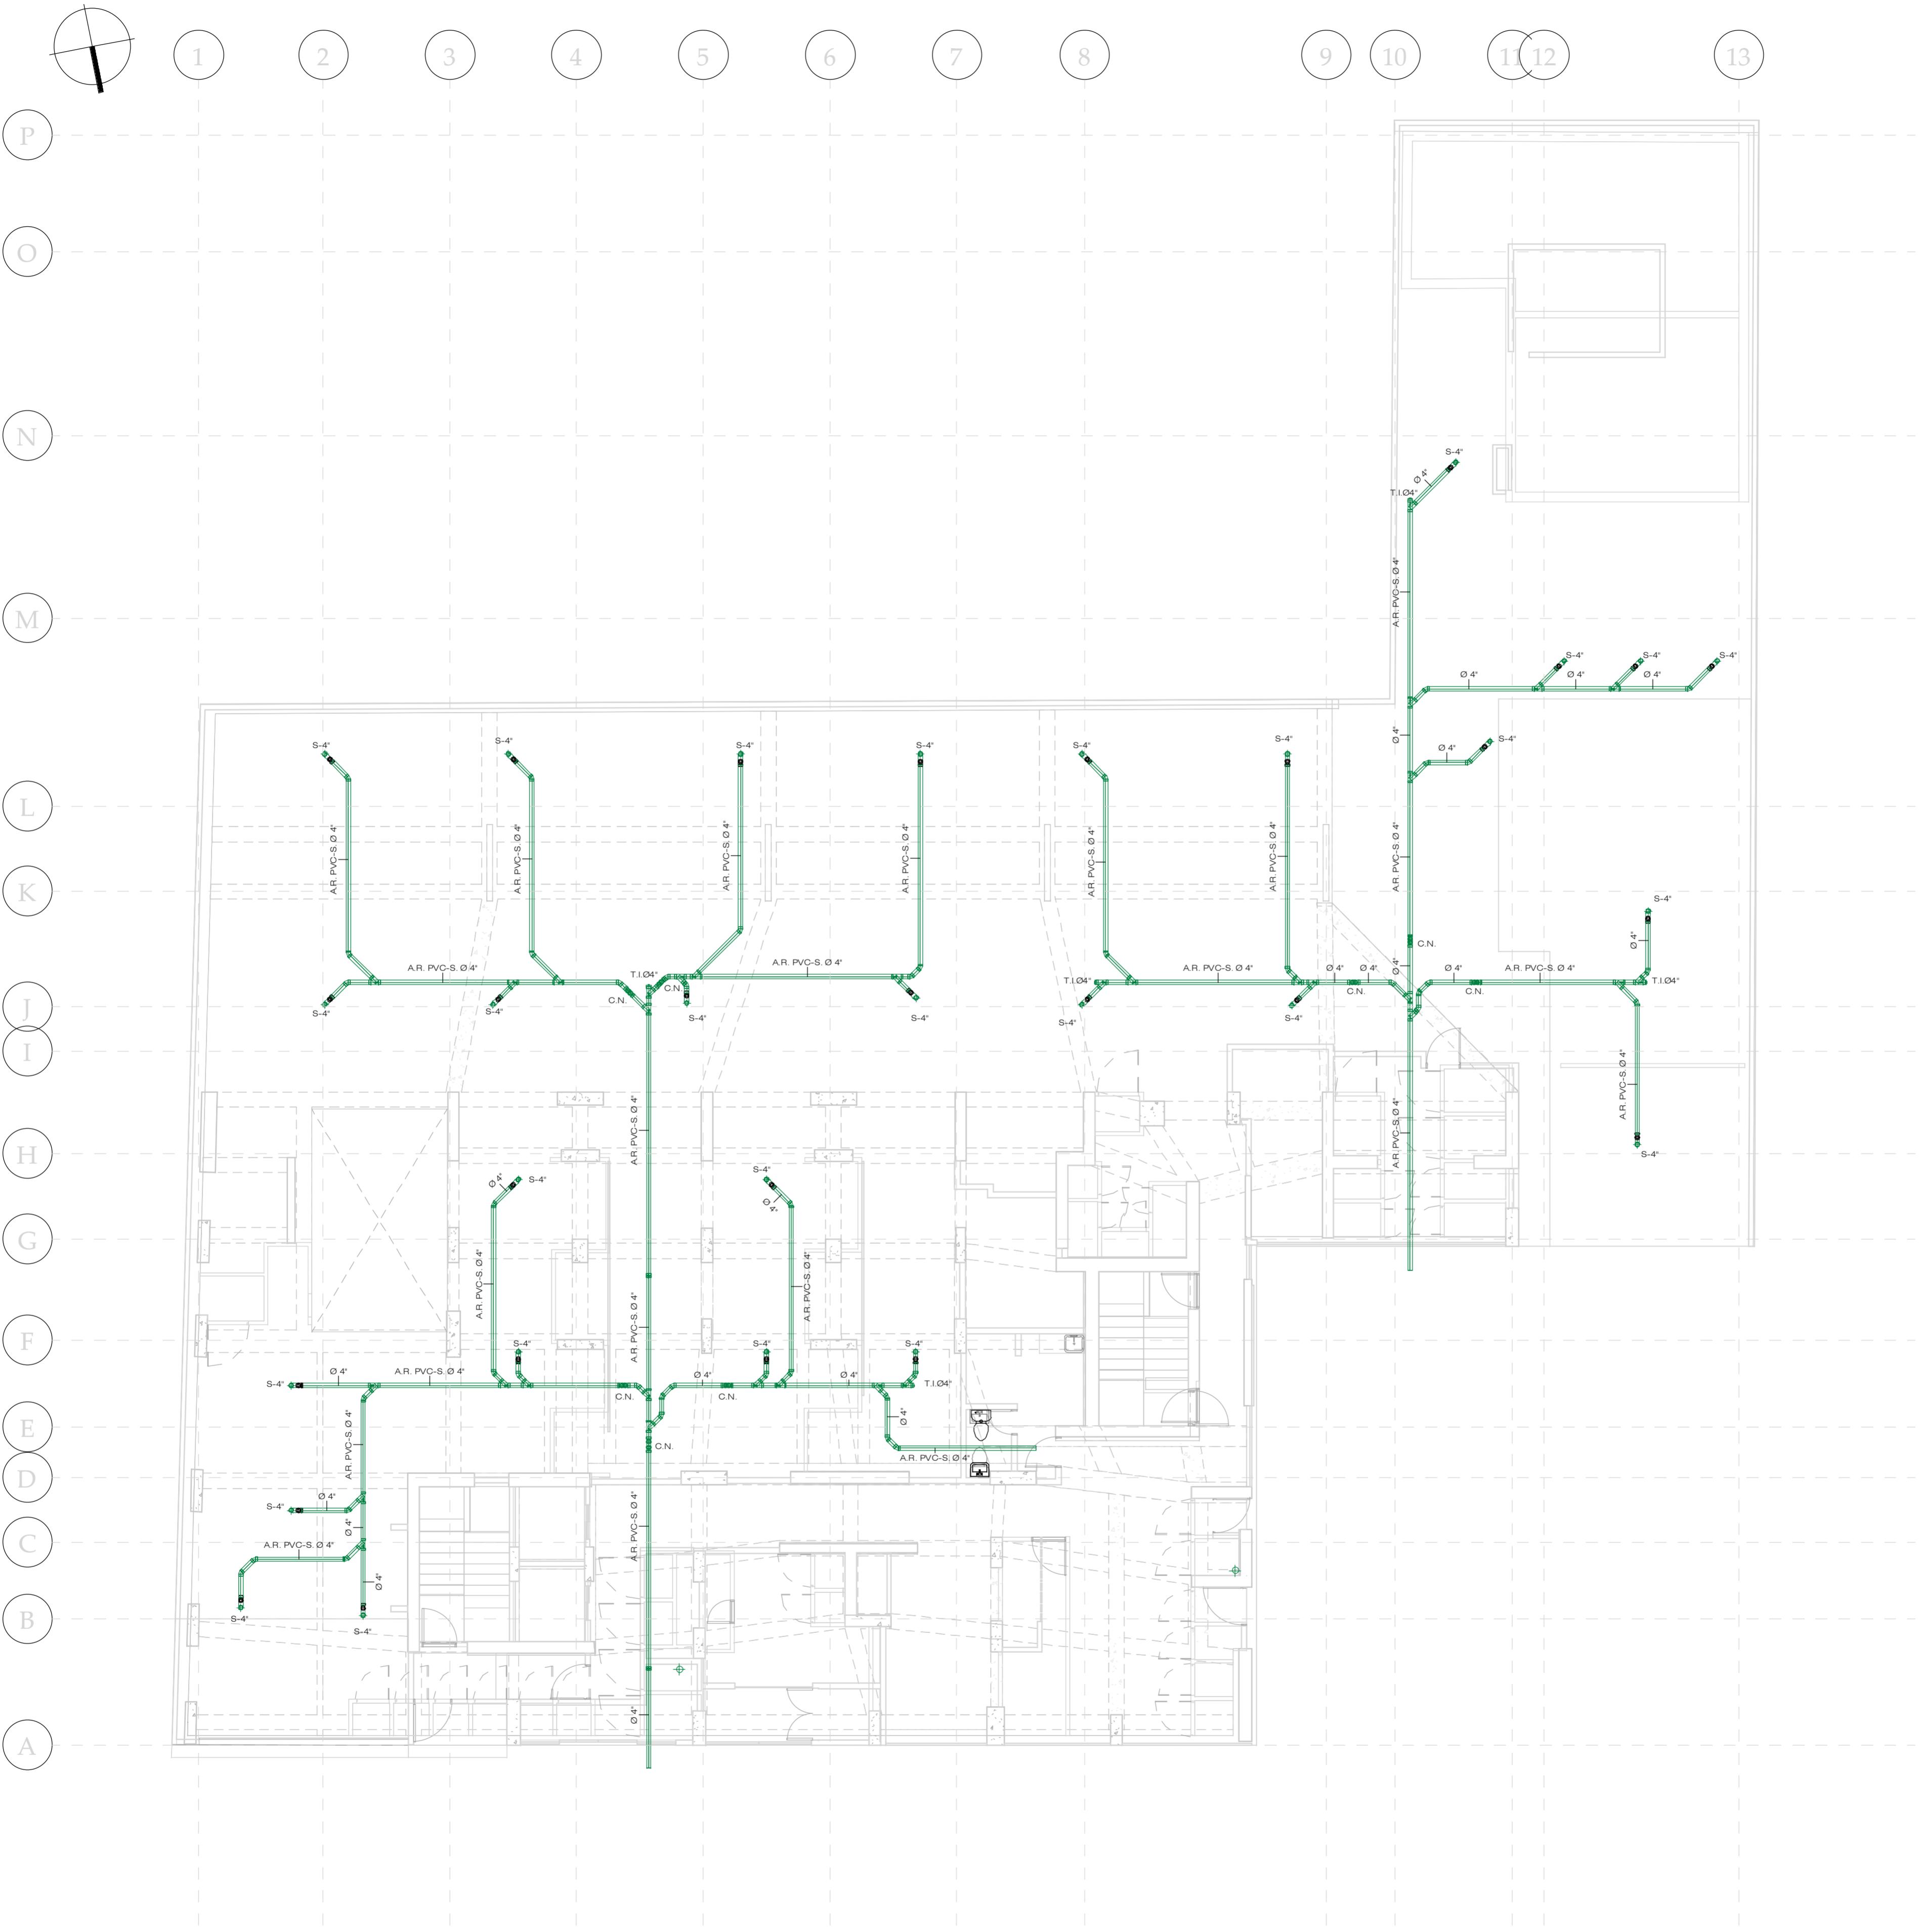


PLANTA DESAGÜES  
Nivel 1

1 : 100

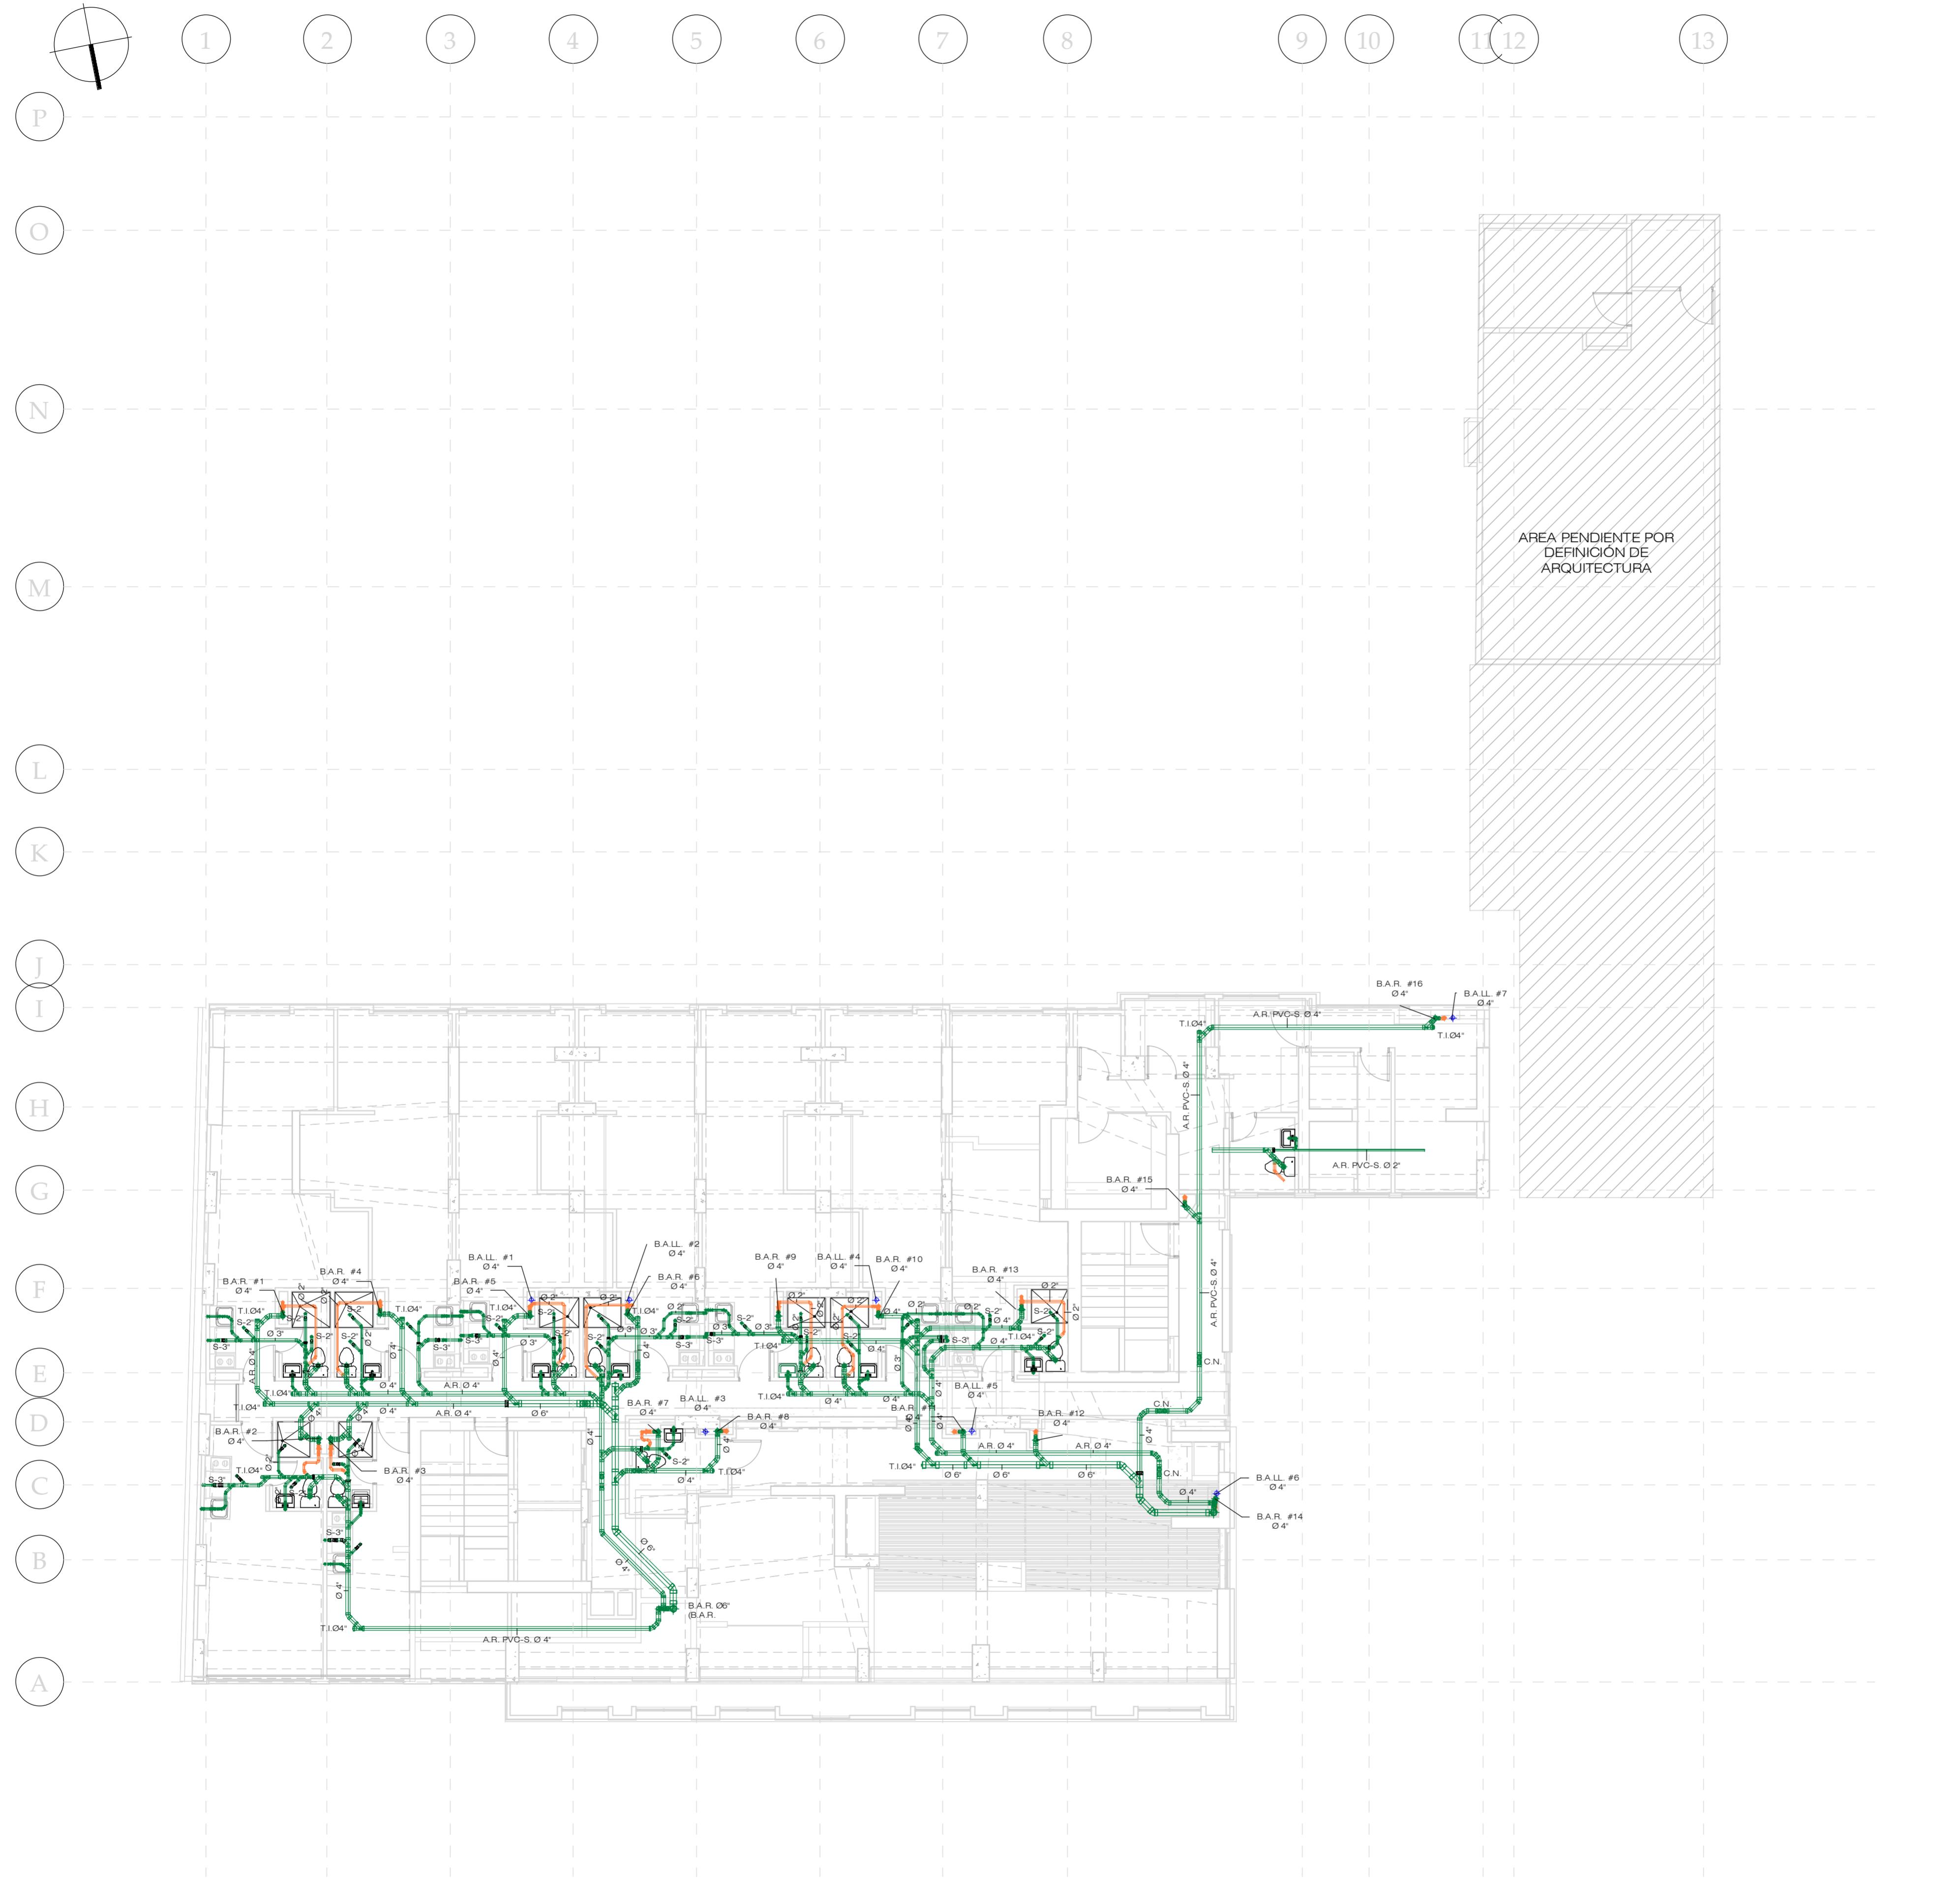


PLANTA DESAGÜES  
Nivel 2

1 : 100

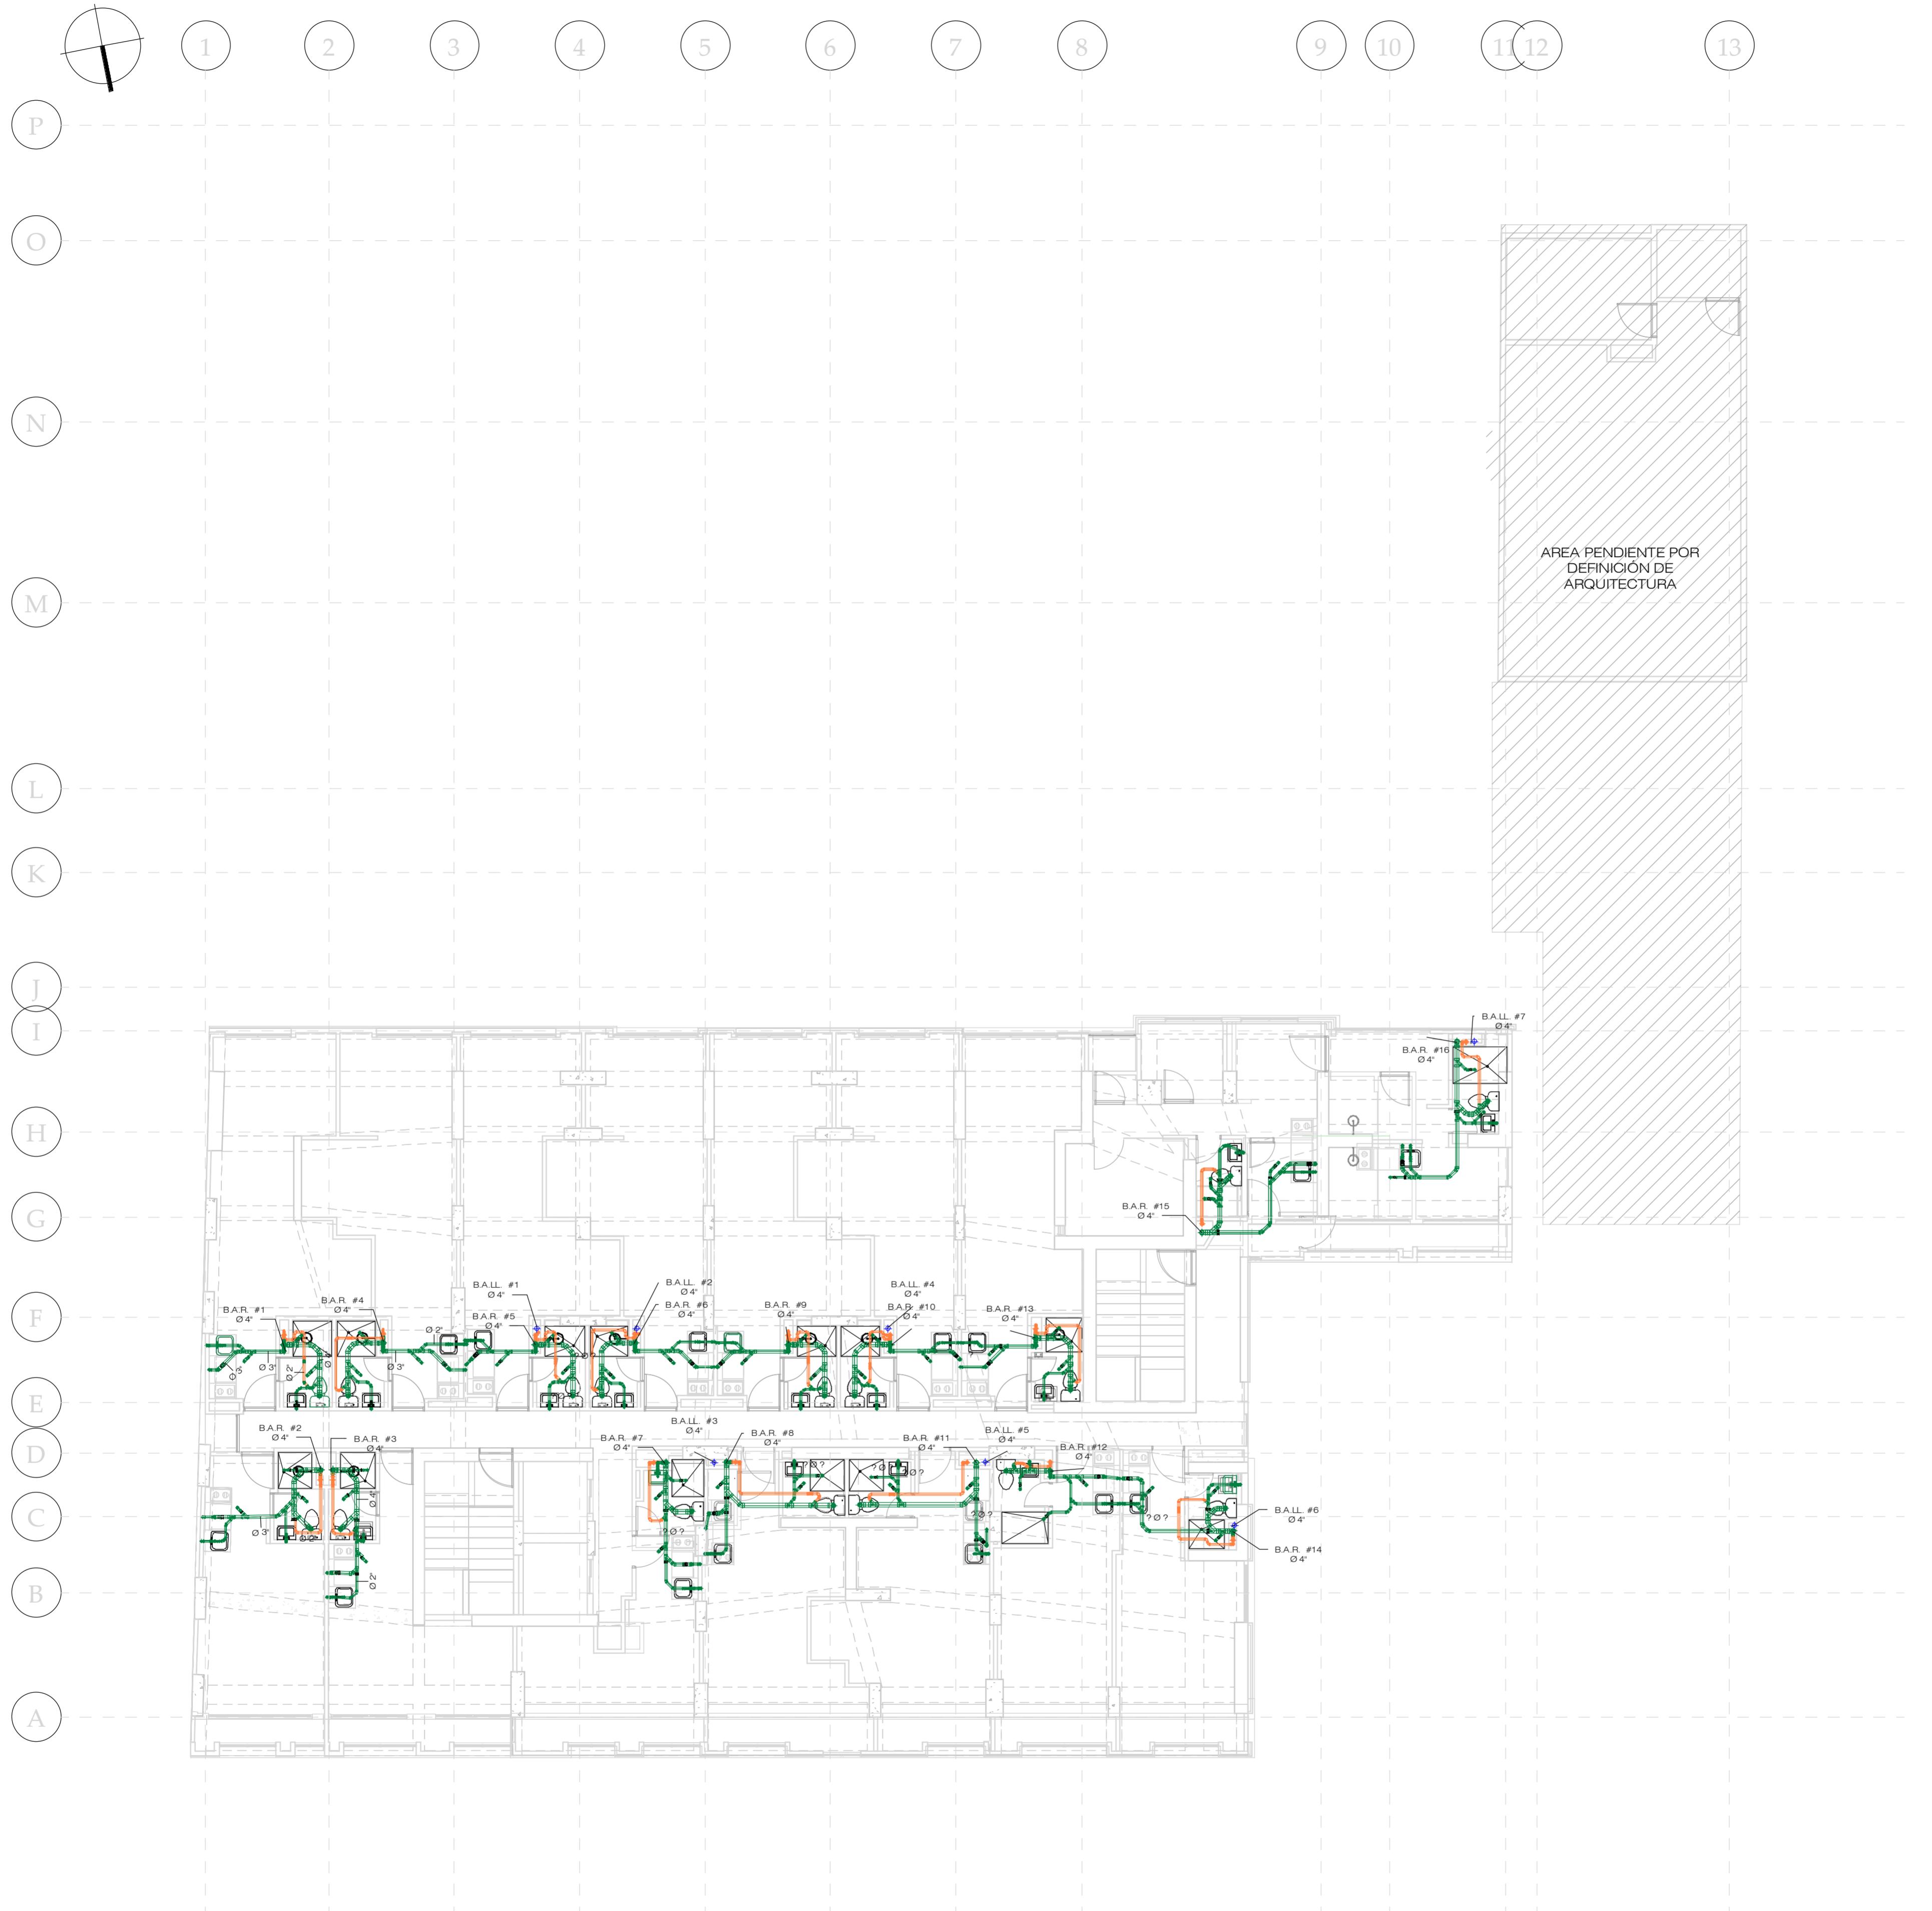


PLANTA DESAGÜES  
Nivel 3

1 : 100

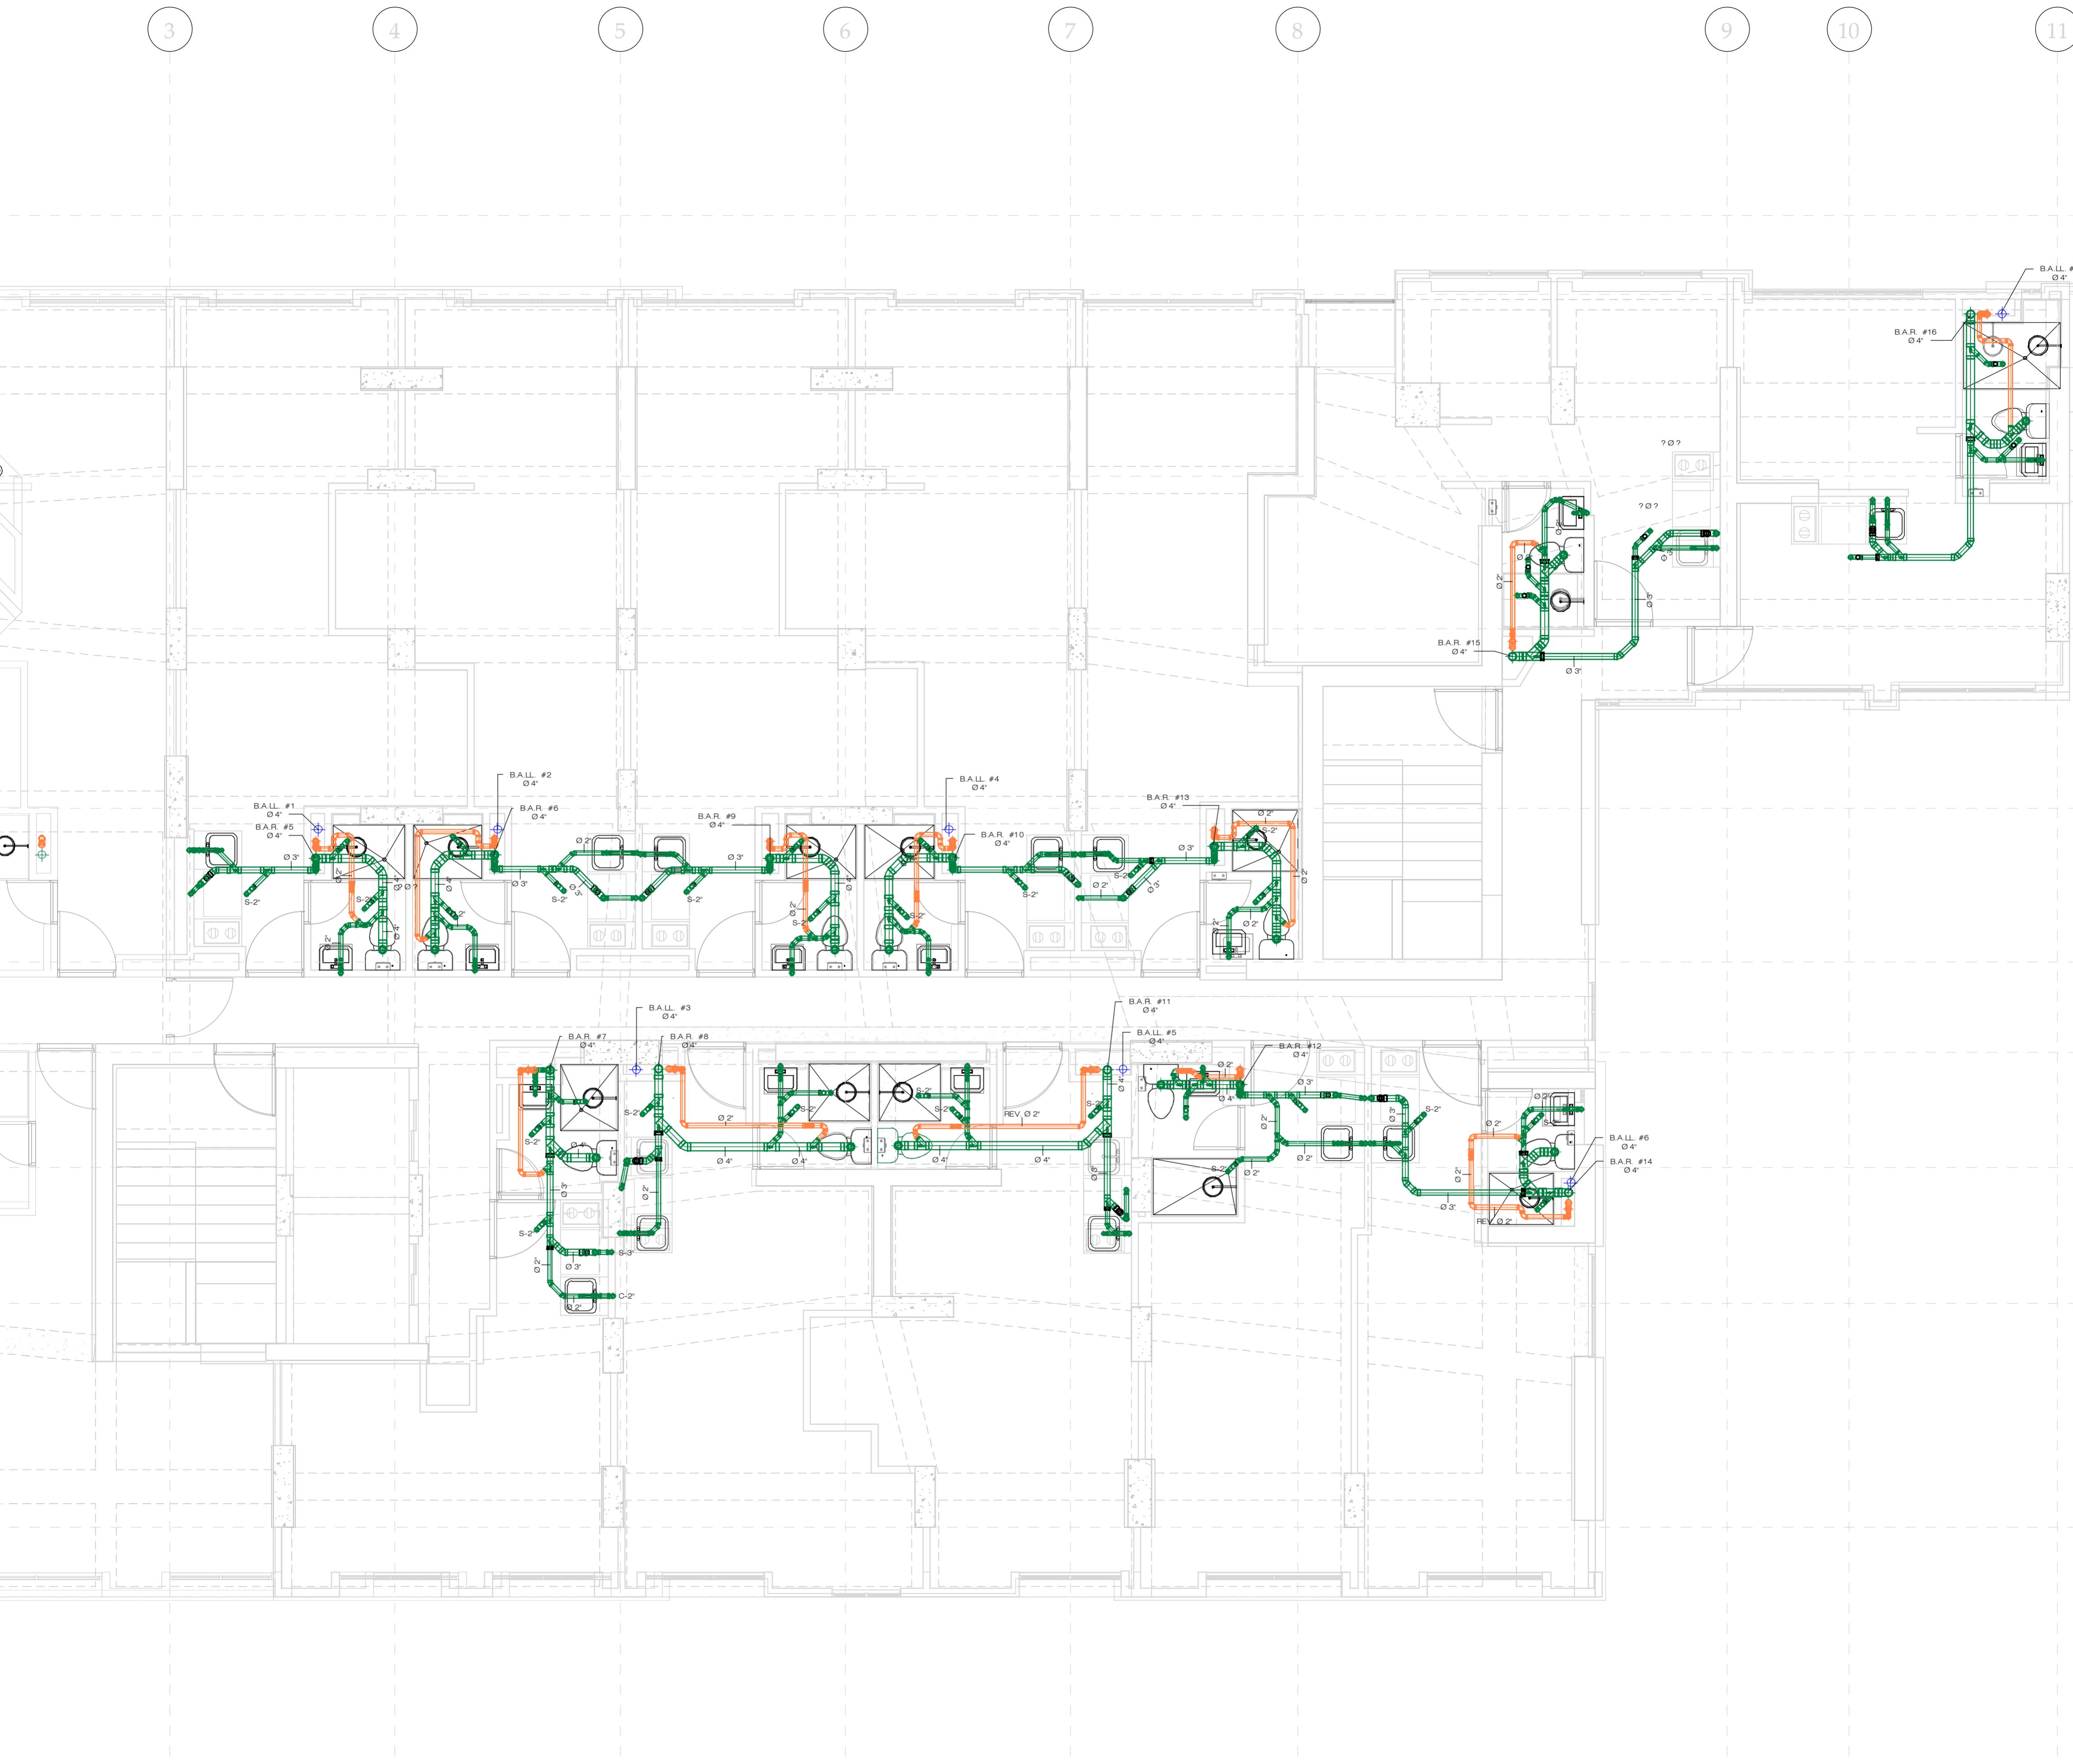


PLANTA DESAGÜES  
Nivel 5

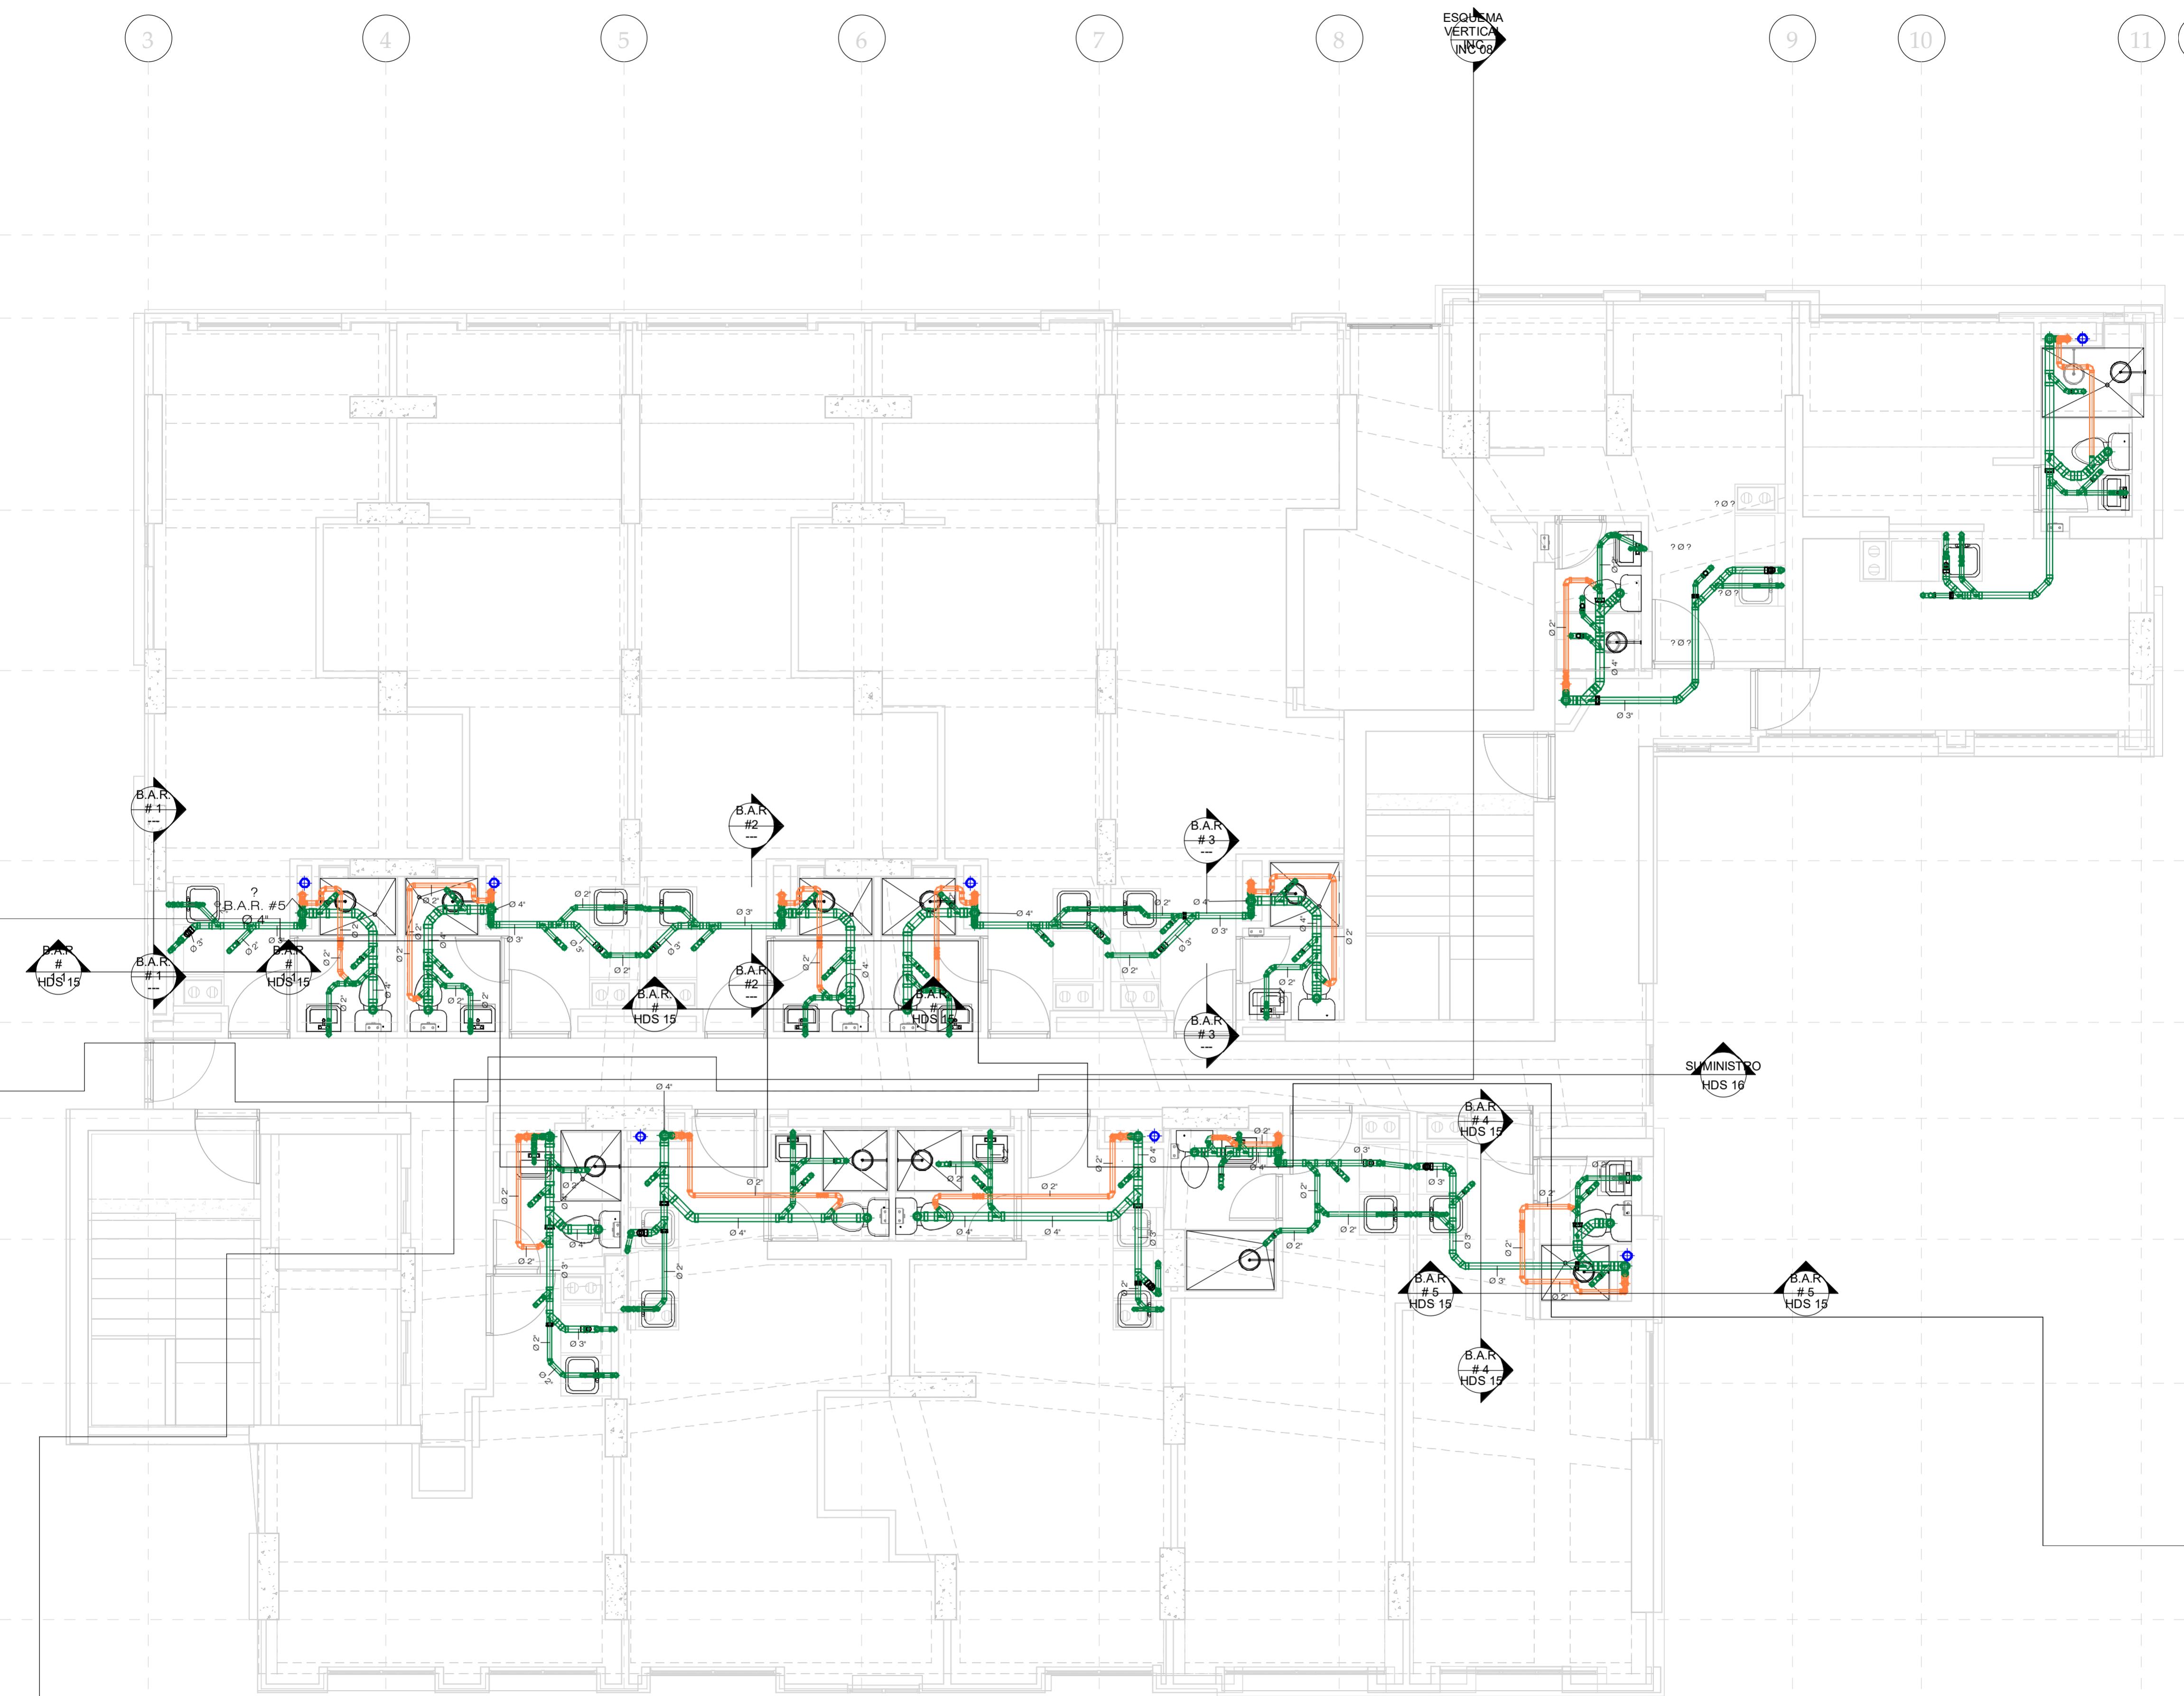


PLANTA DESAGÜES  
PISO TIPO 6-19

1 : 50

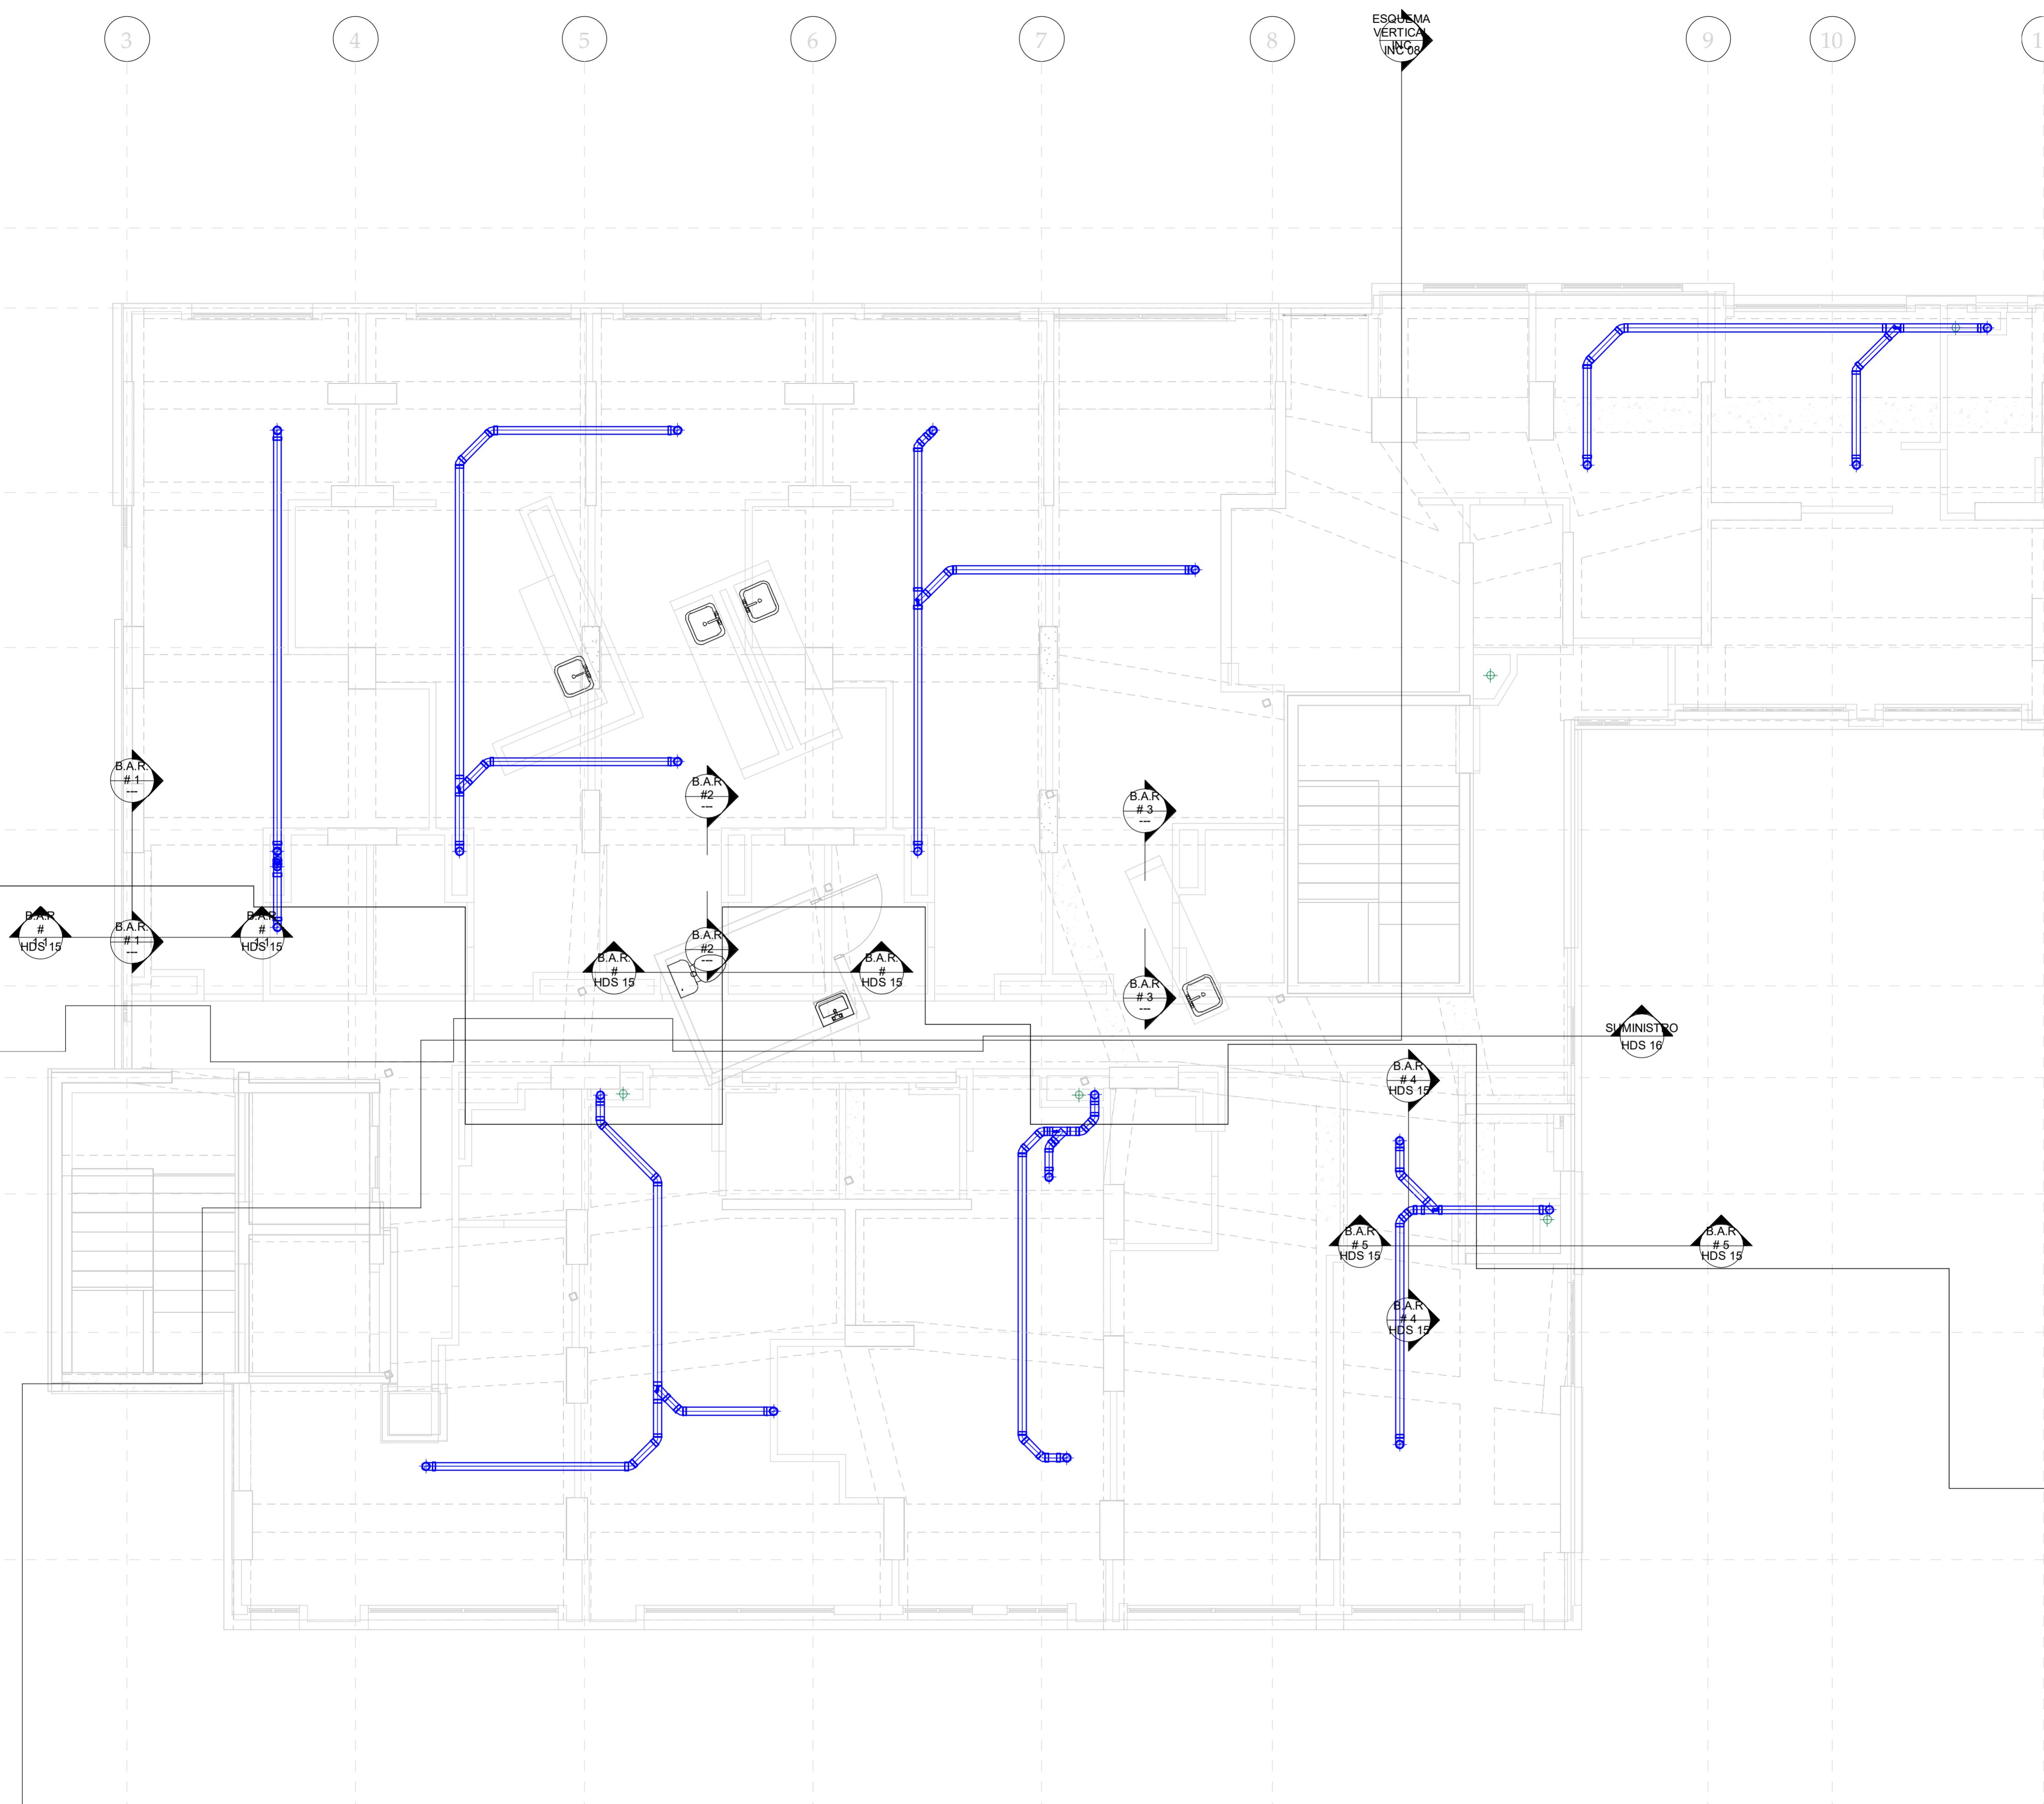

PLANTA DESAGÜES  
CUBIERTA

1 : 50

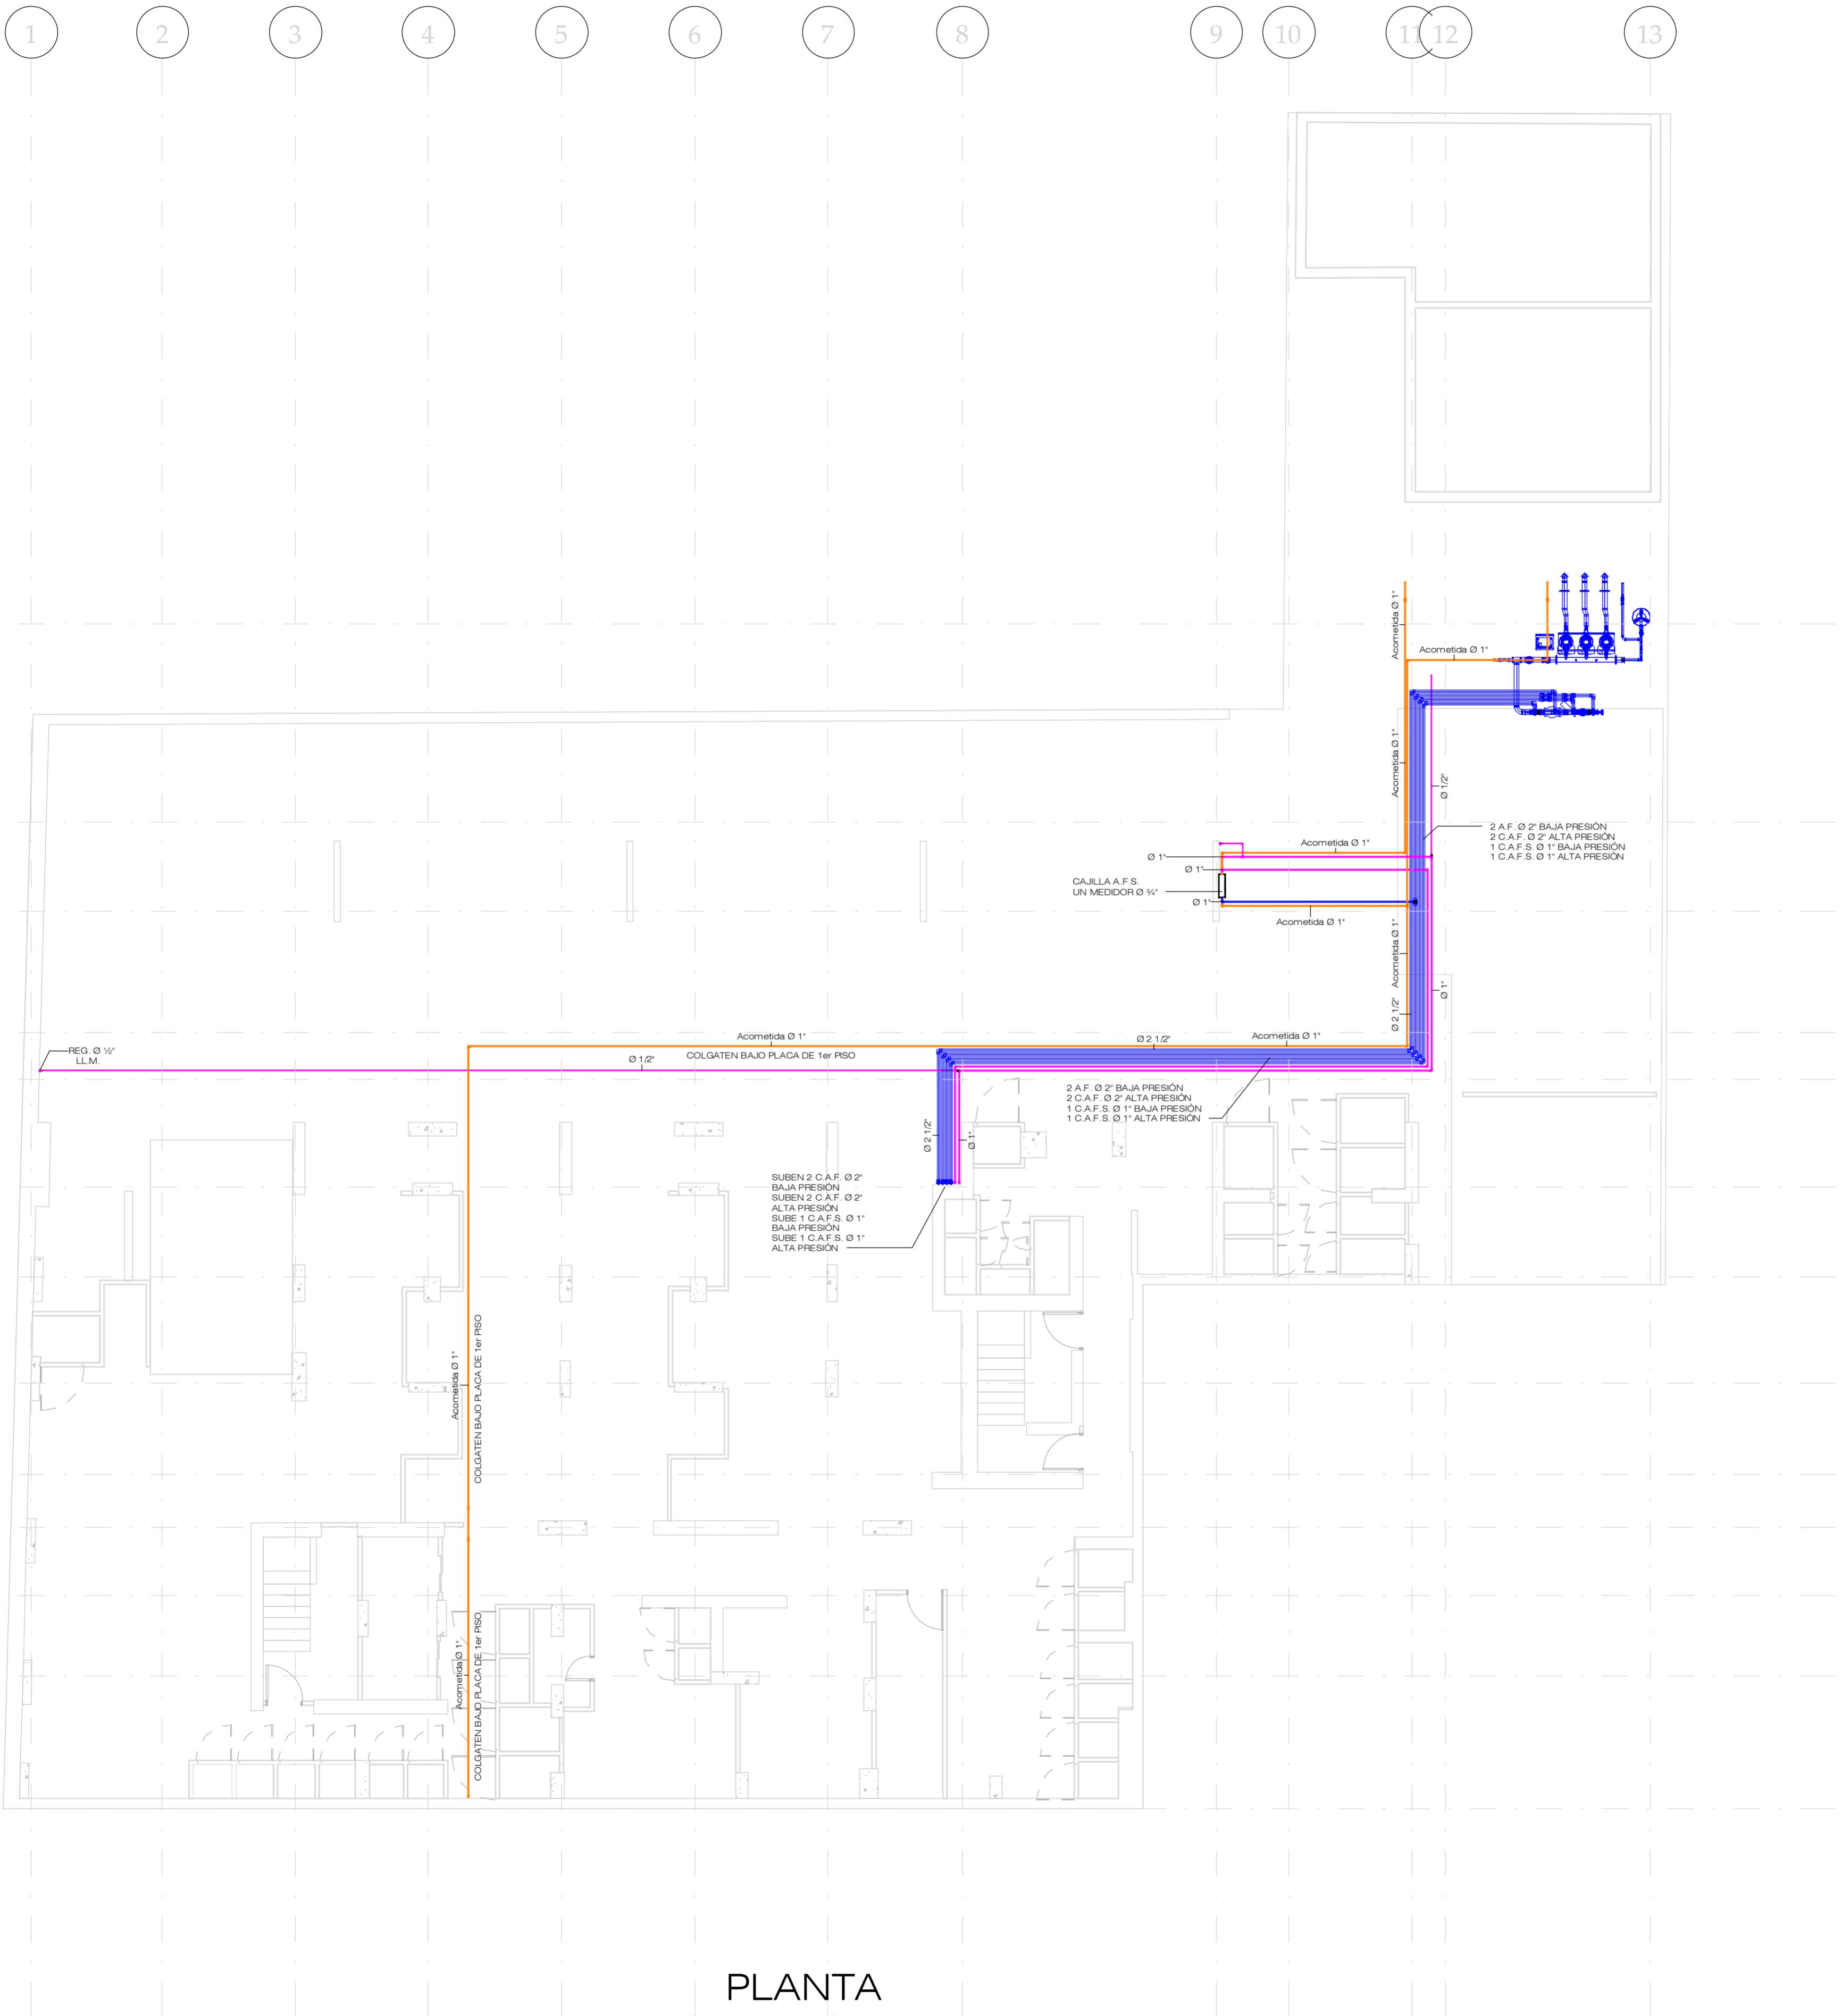

PLANTA  
SUMINISTRO  
SOTANO

1 : 100

N

M

L

K

J


H

1

E


B


A

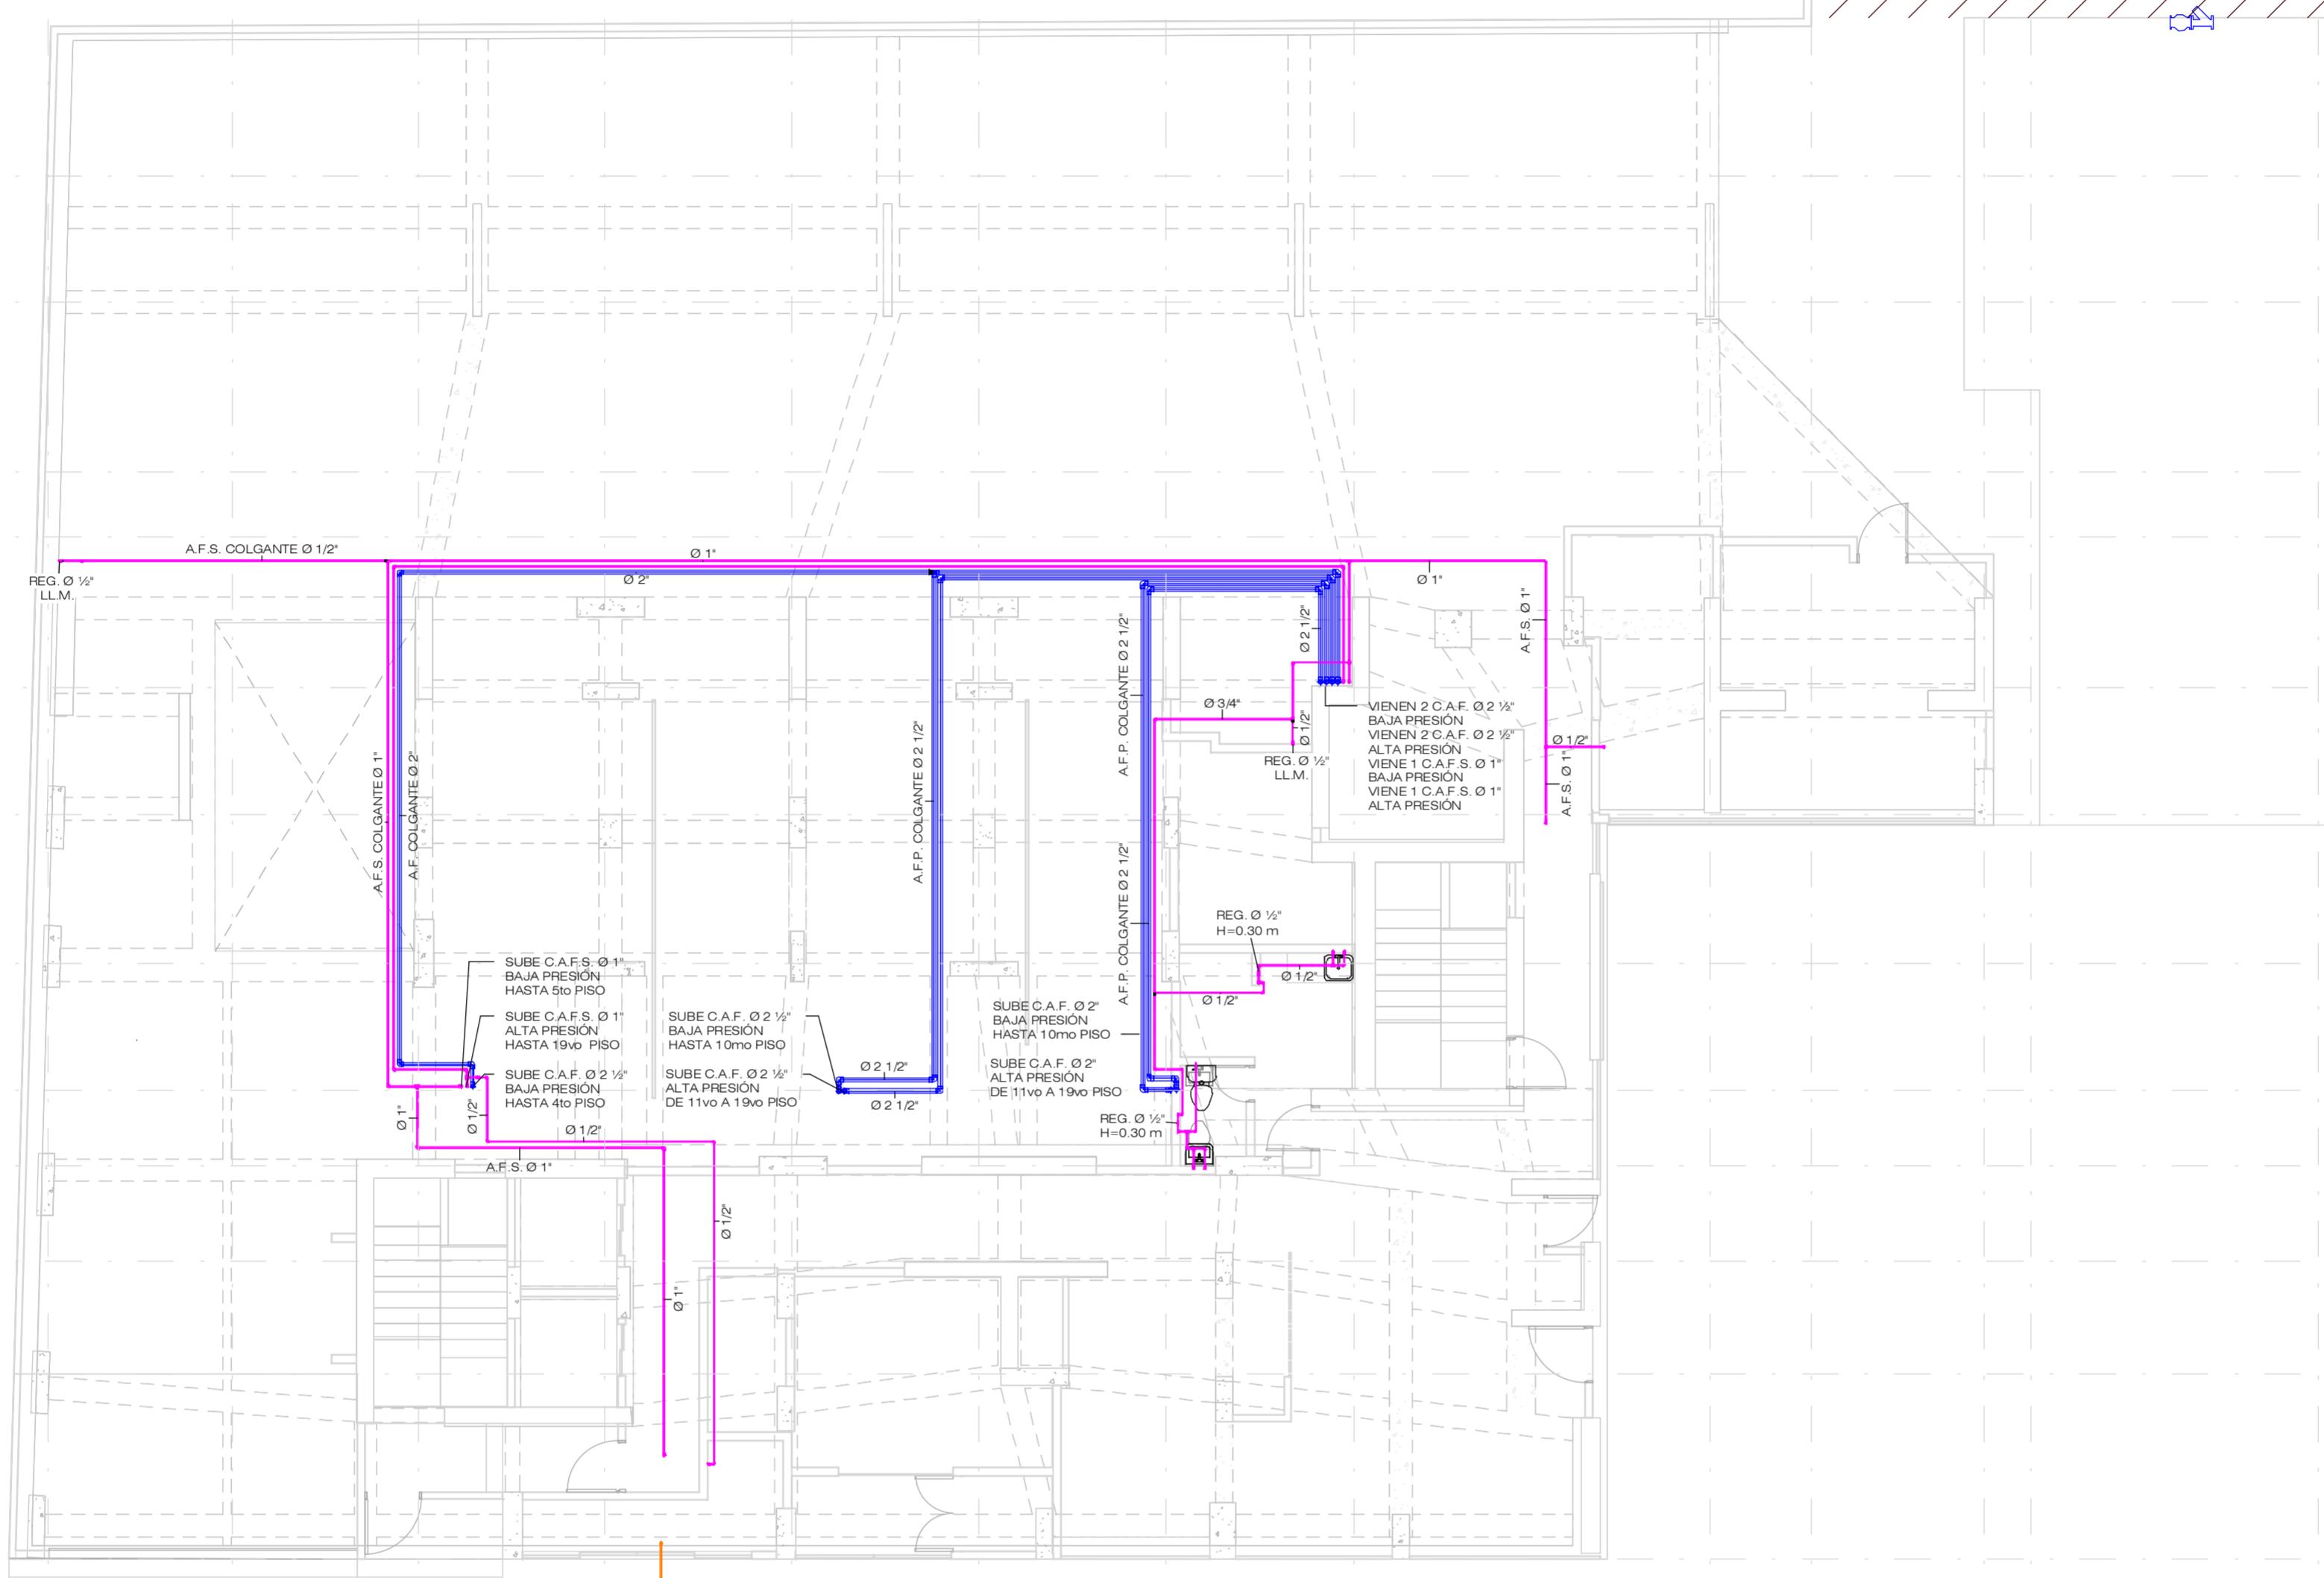


# PLANTA SUMINISTRO Nivel 1

1 : 100

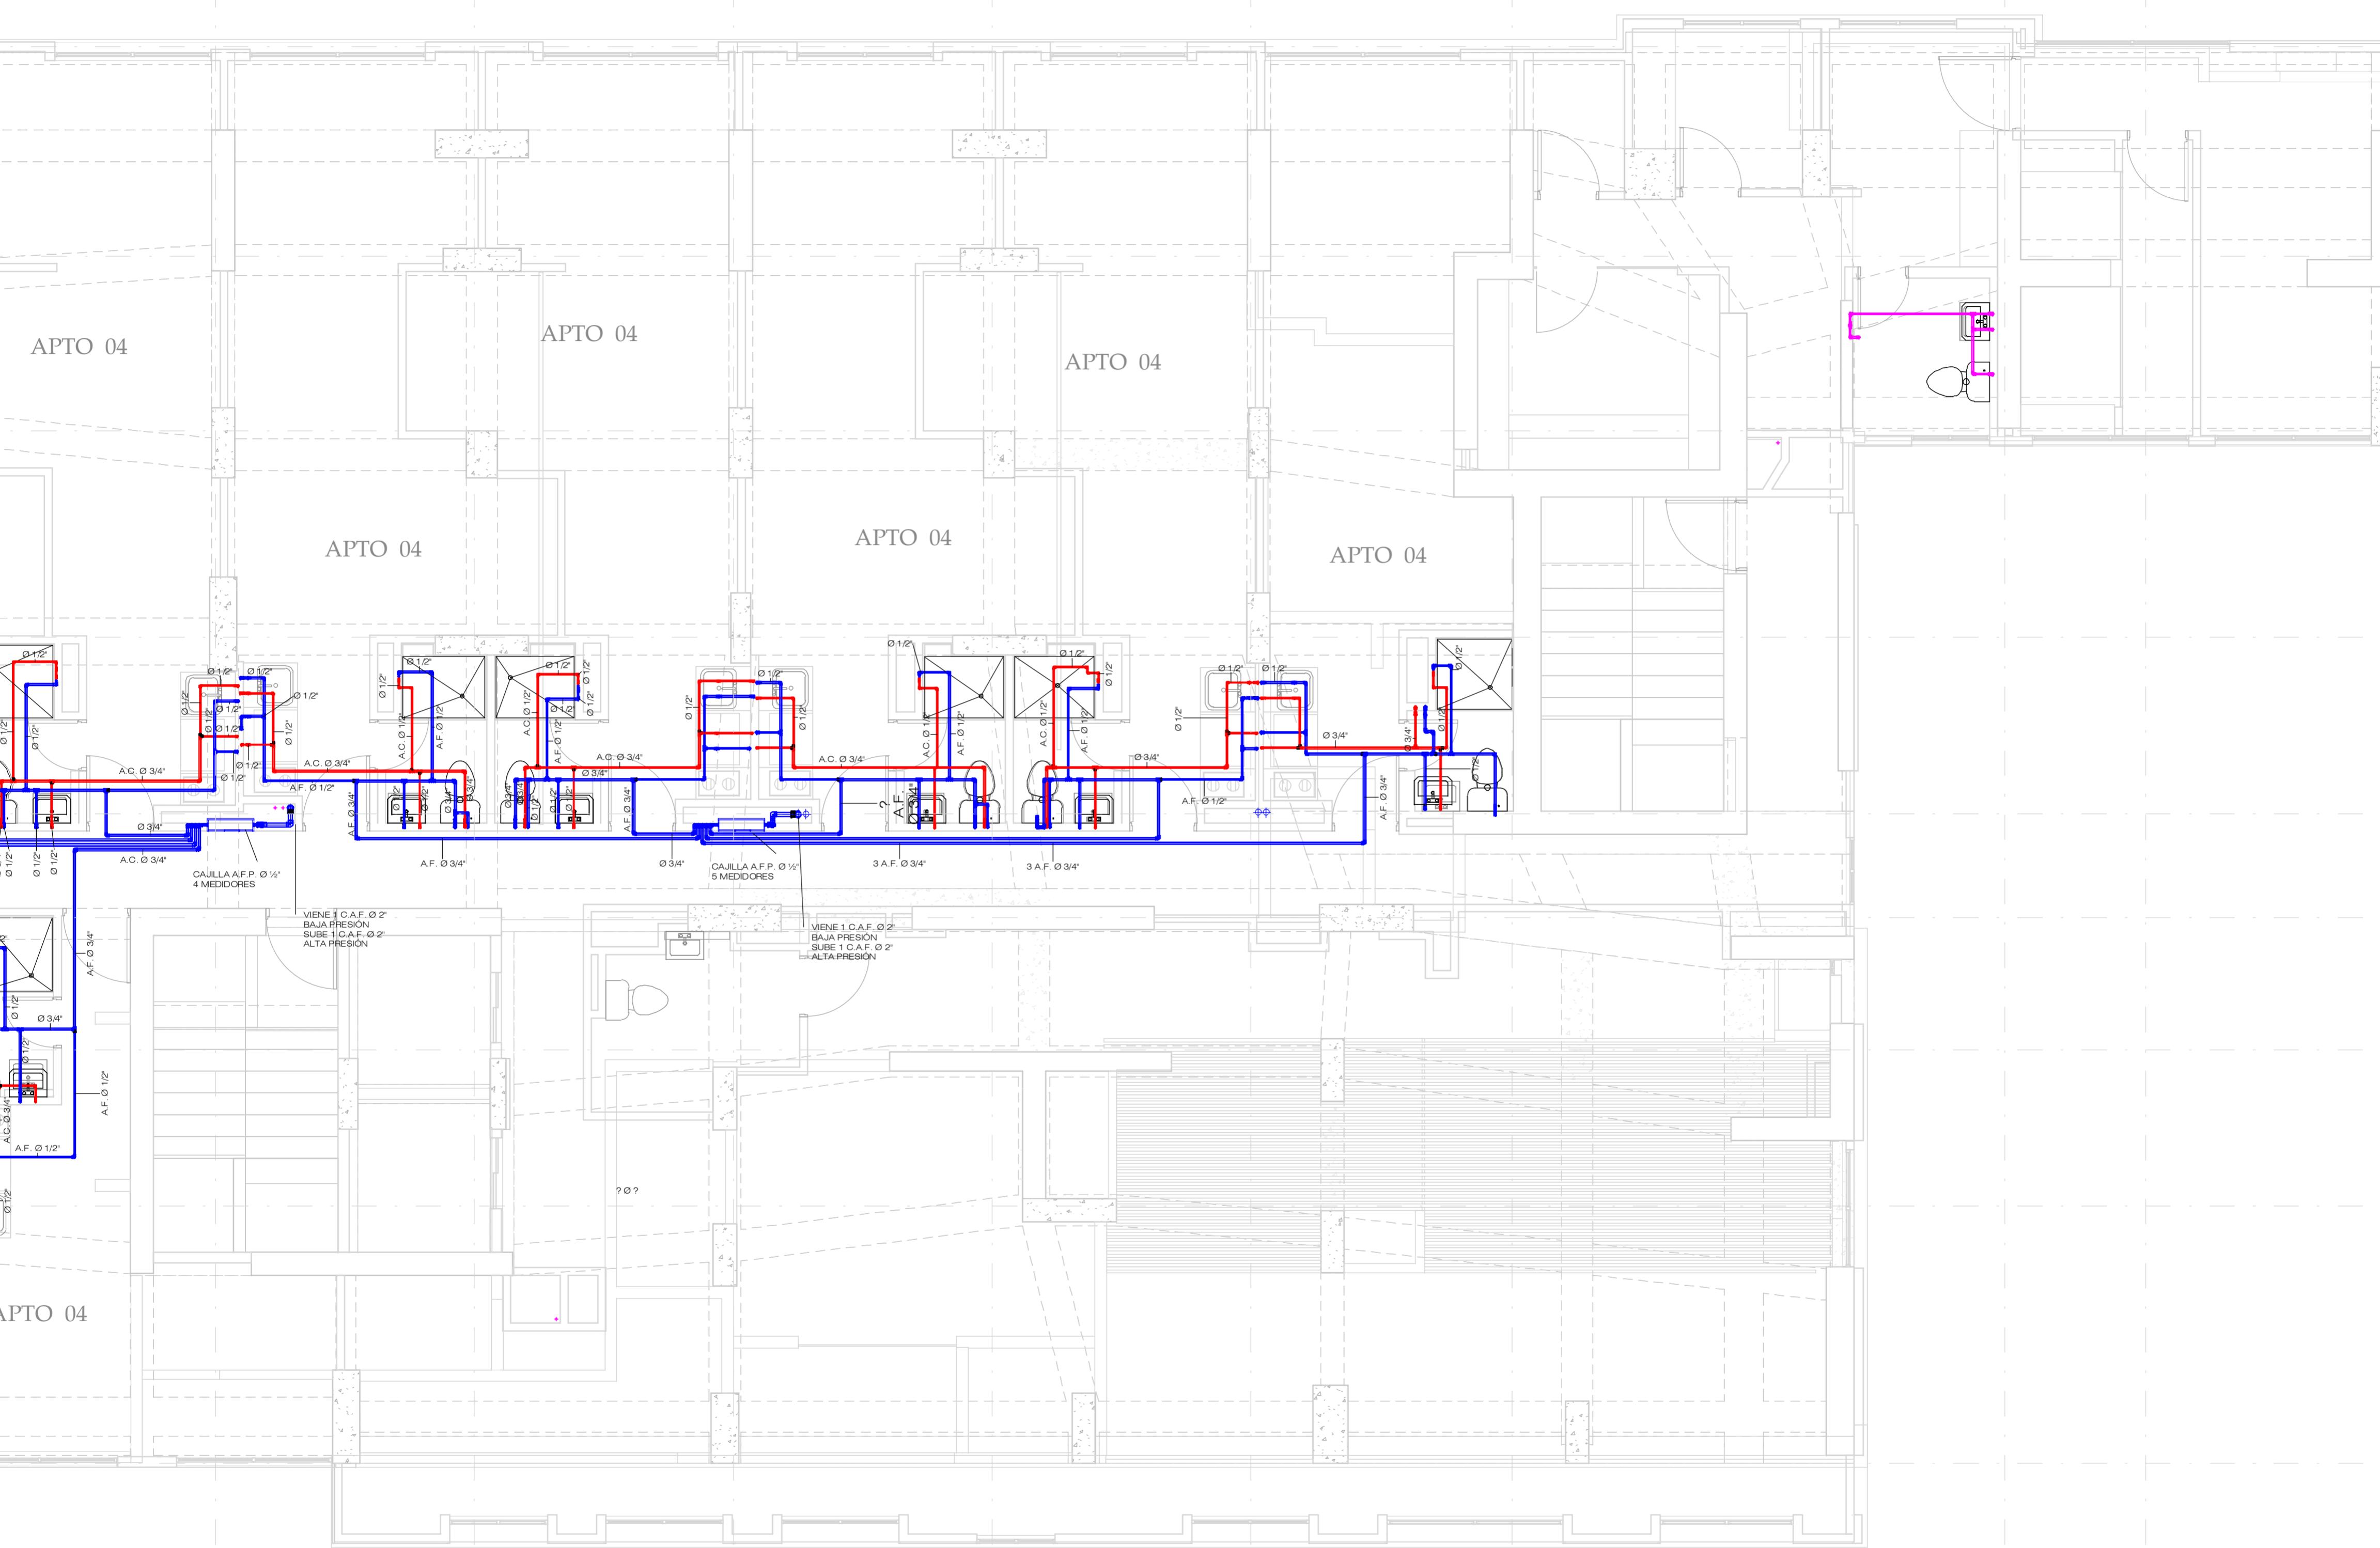


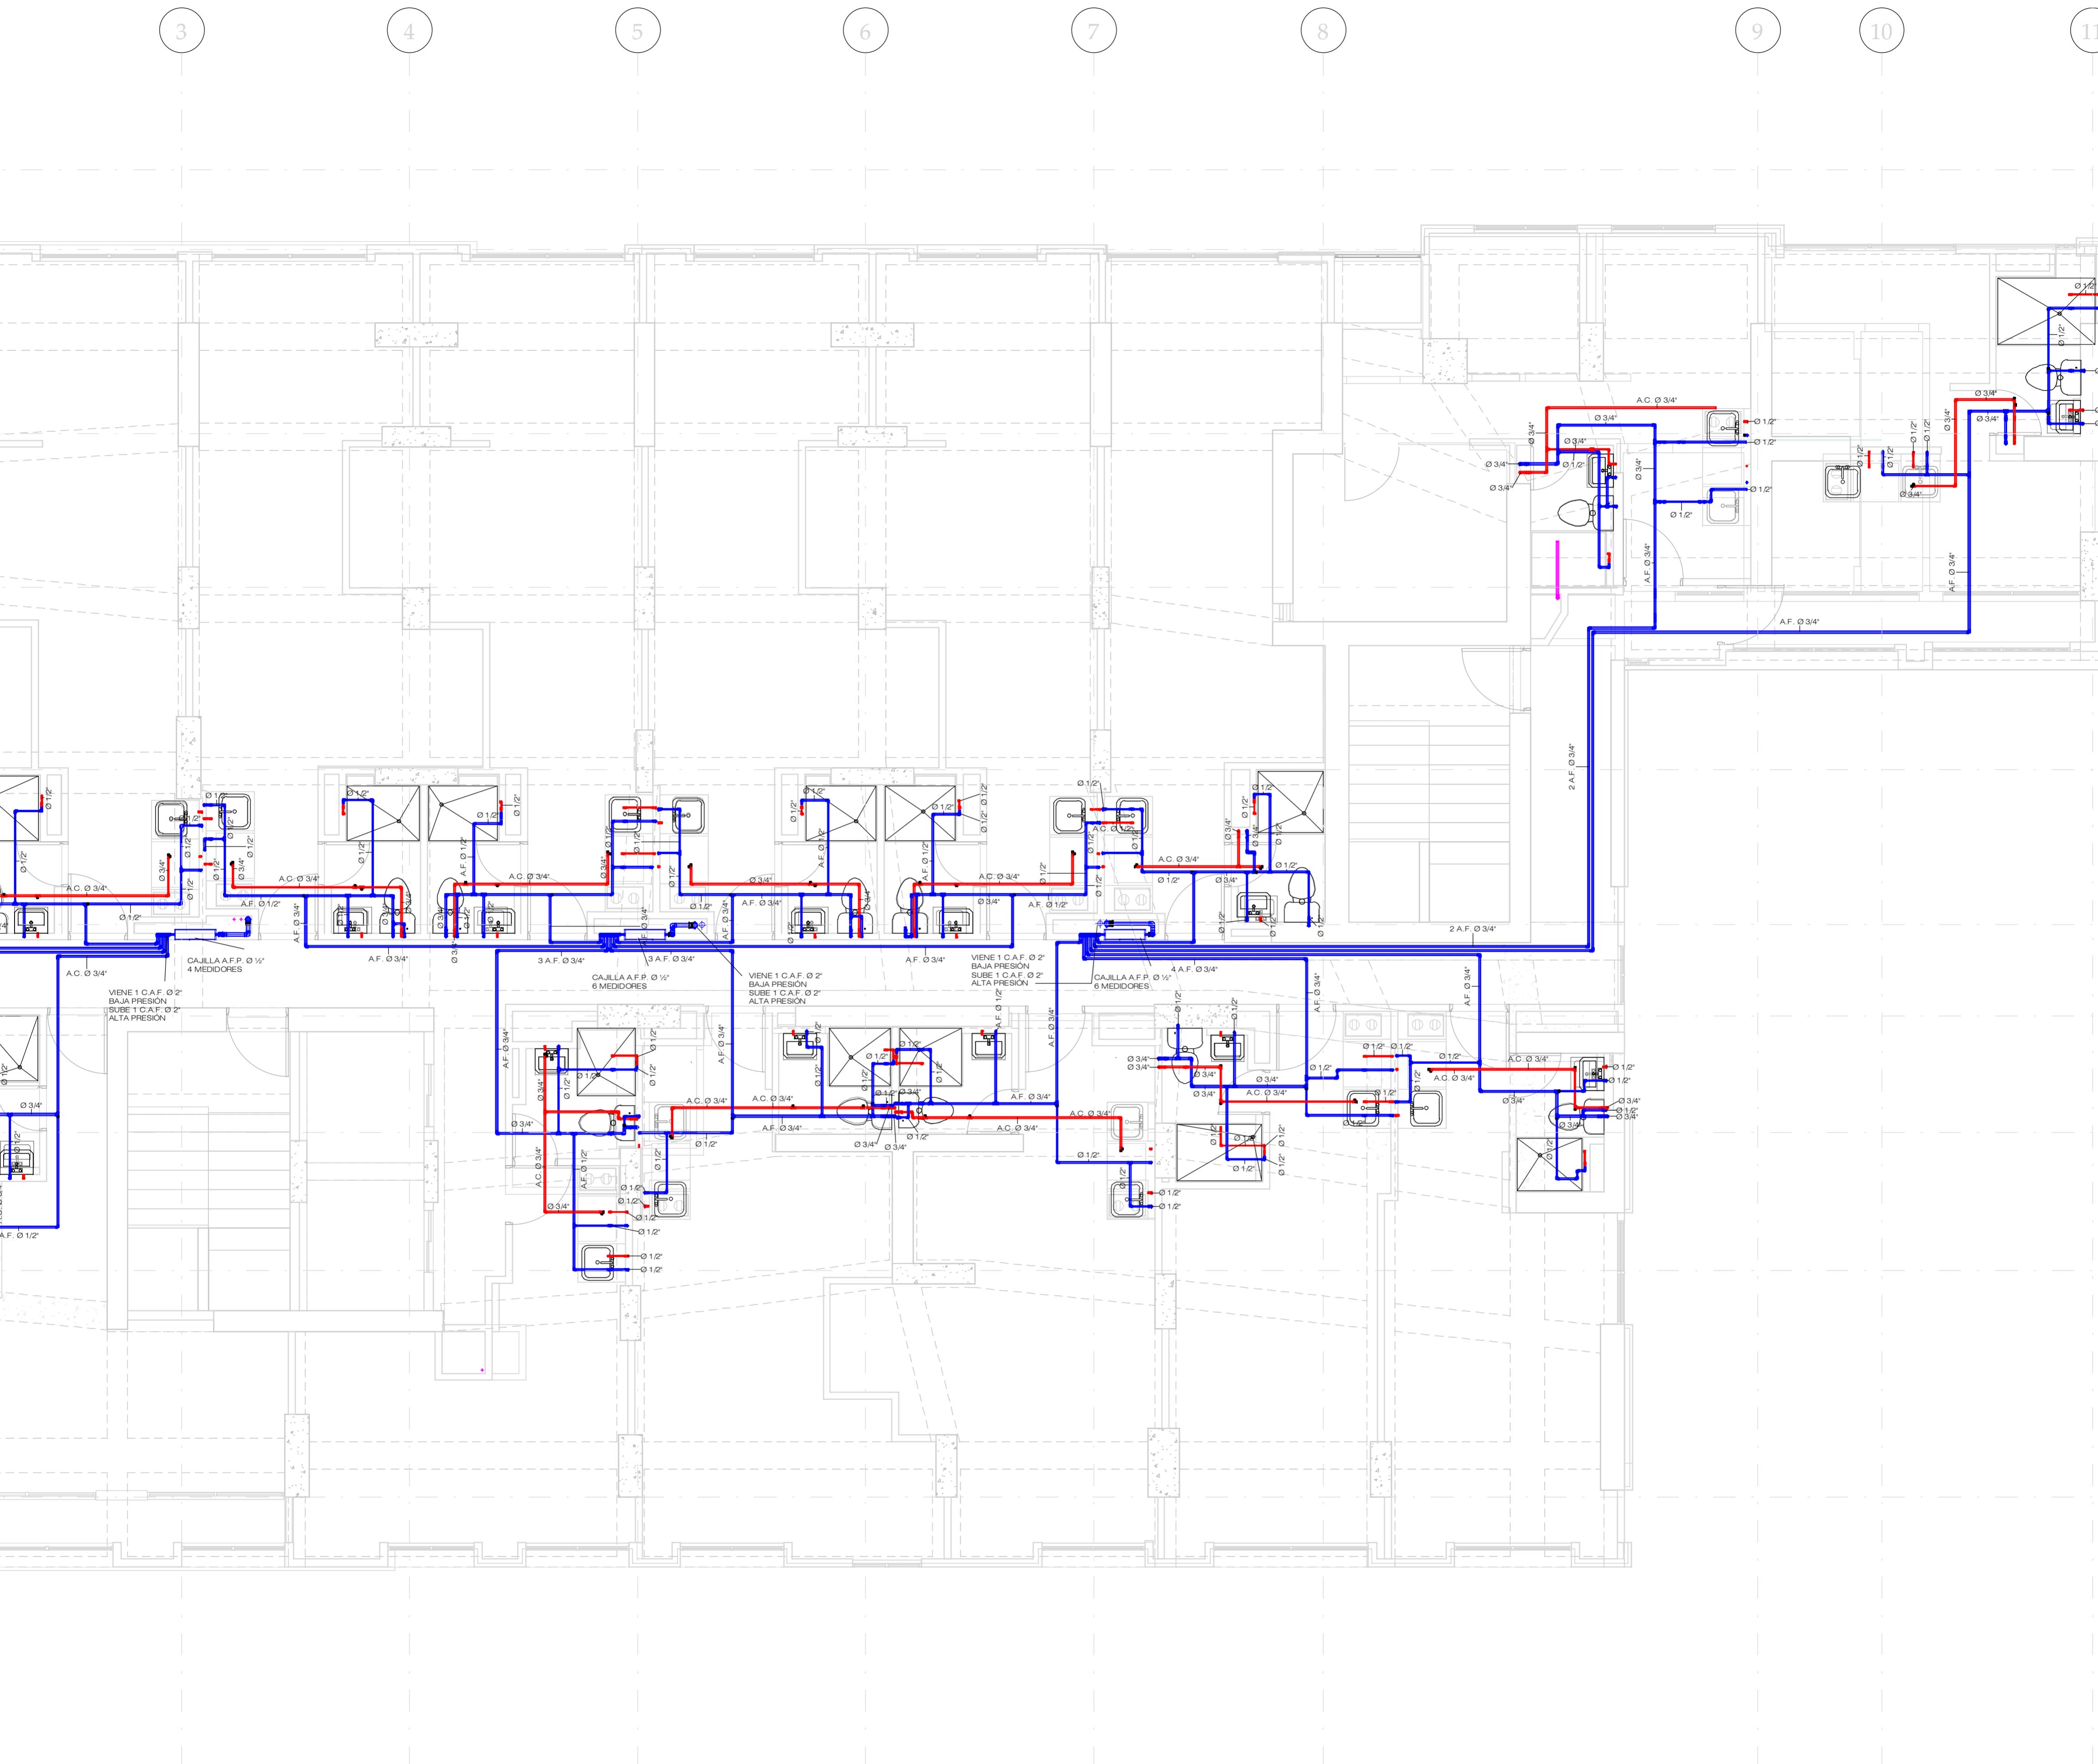

PLANTA

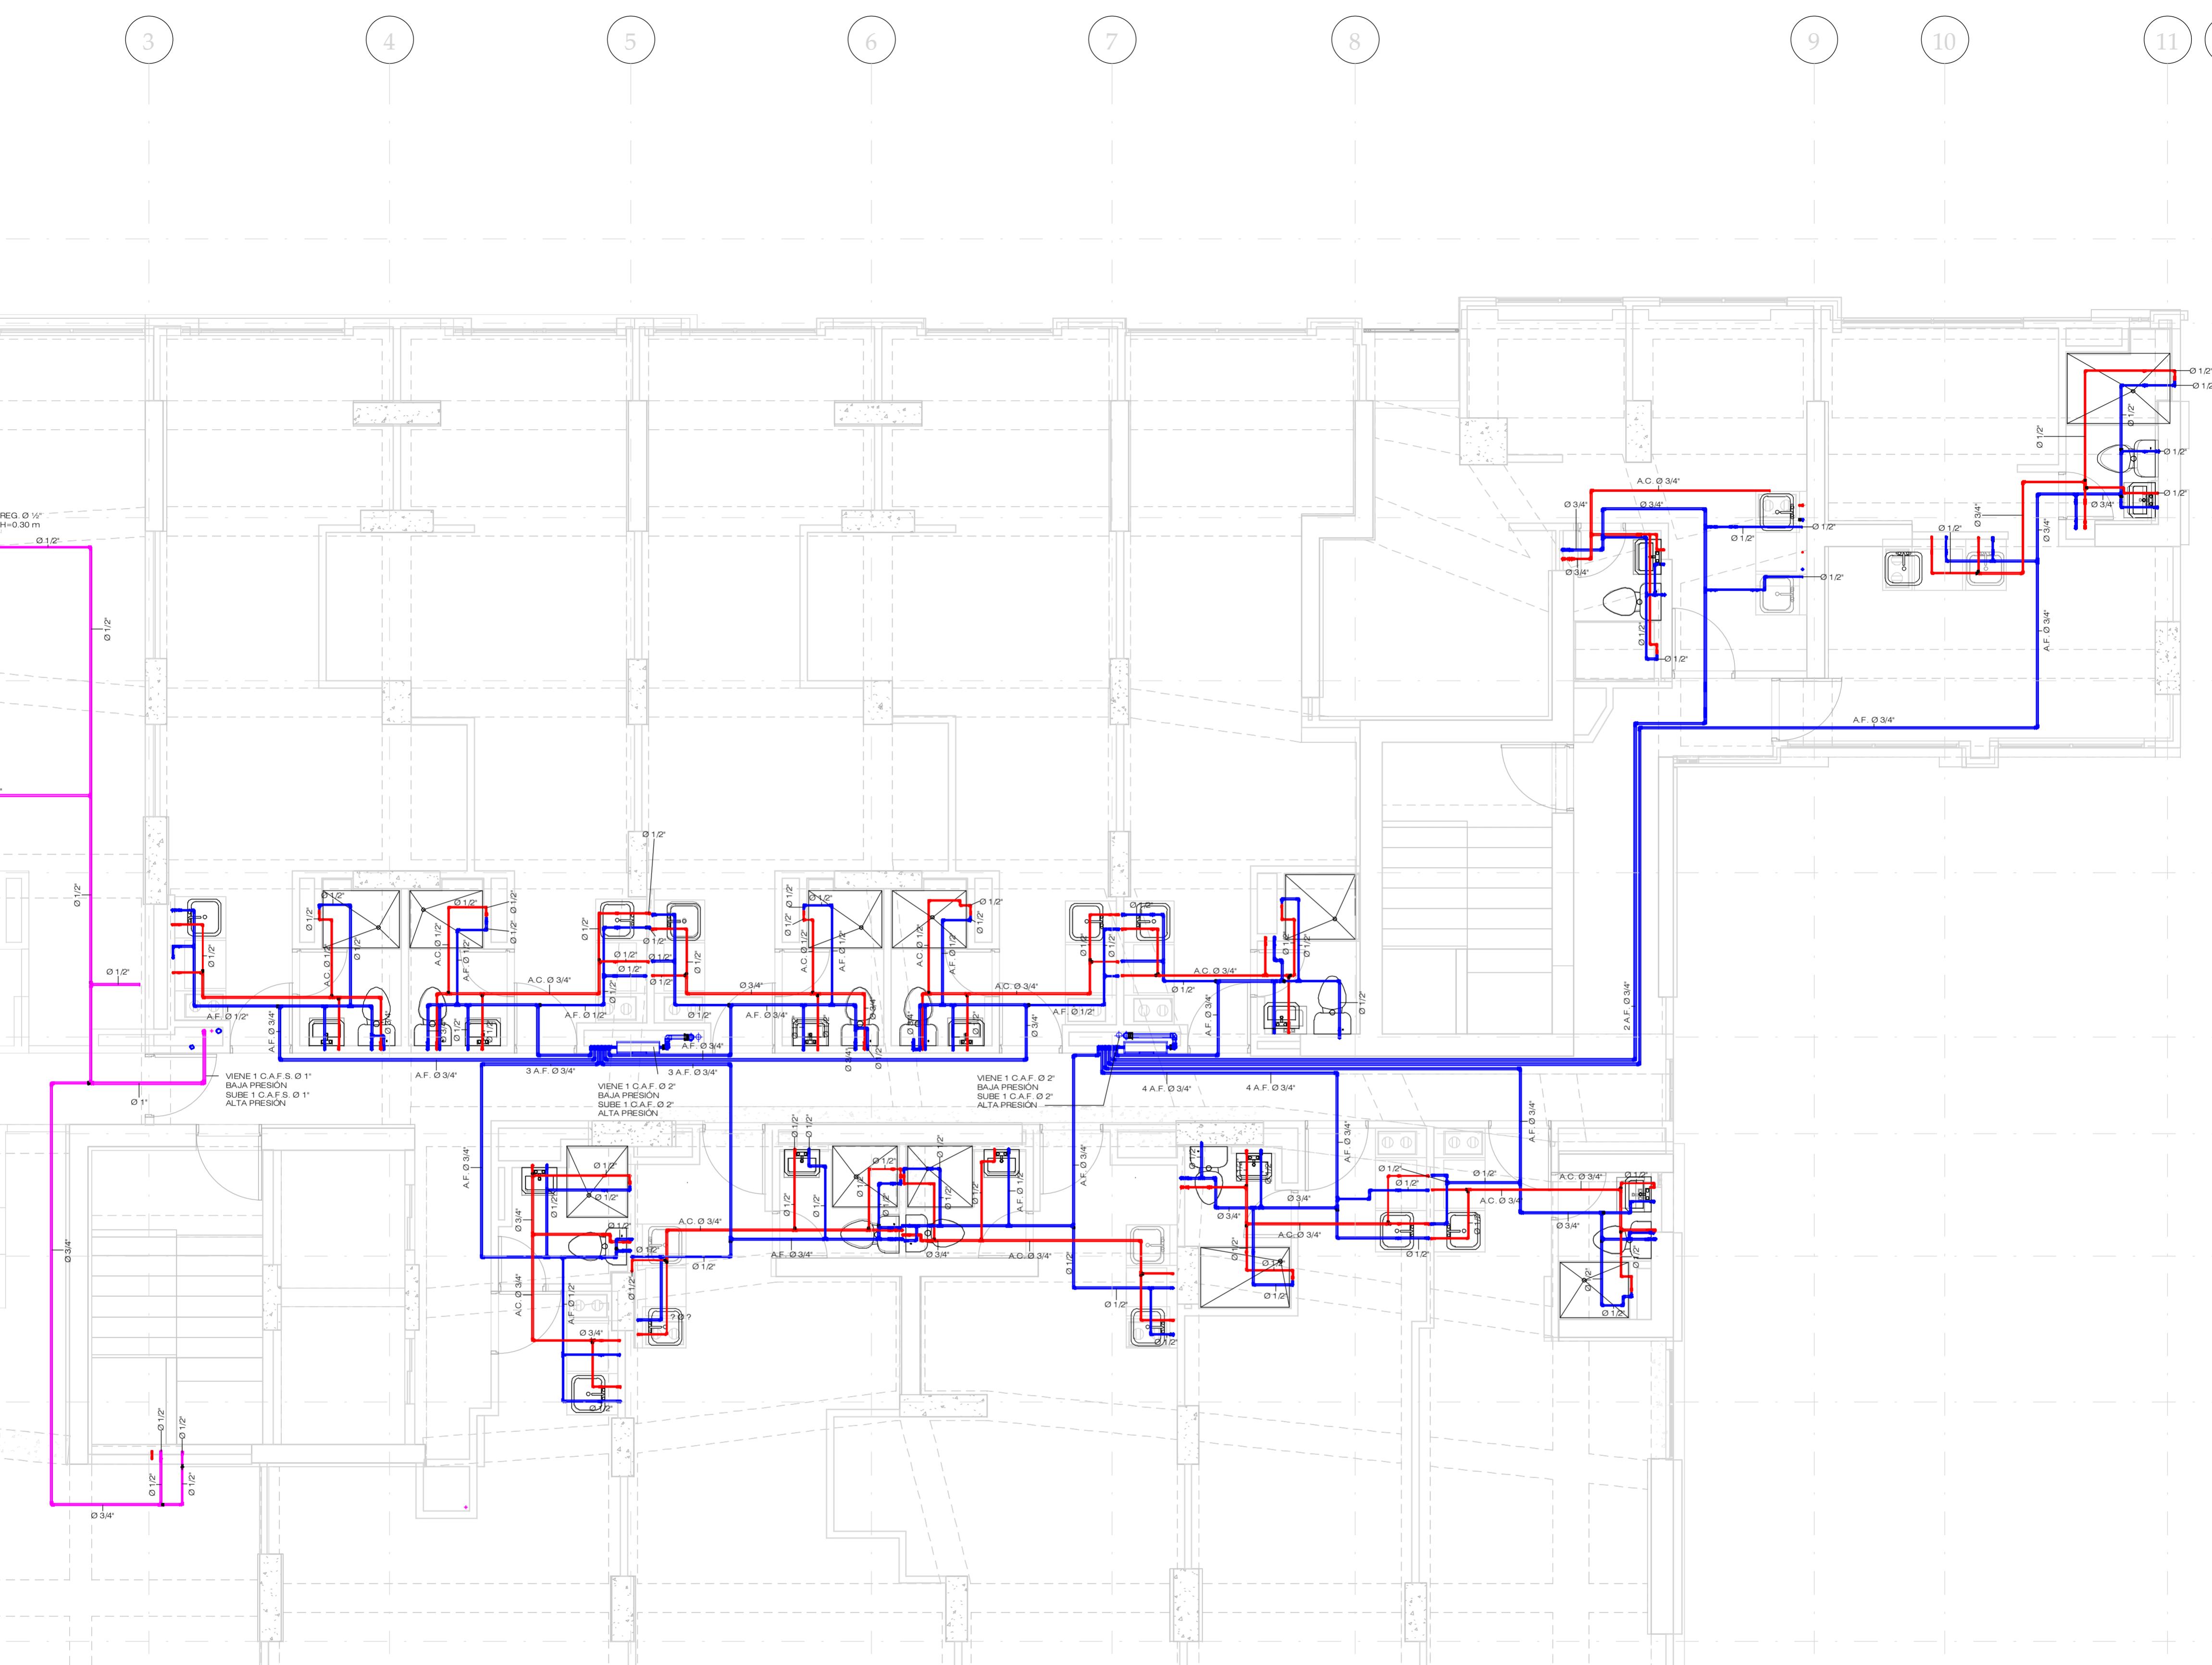

# PLANTA SUMINISTRO Nivel 5

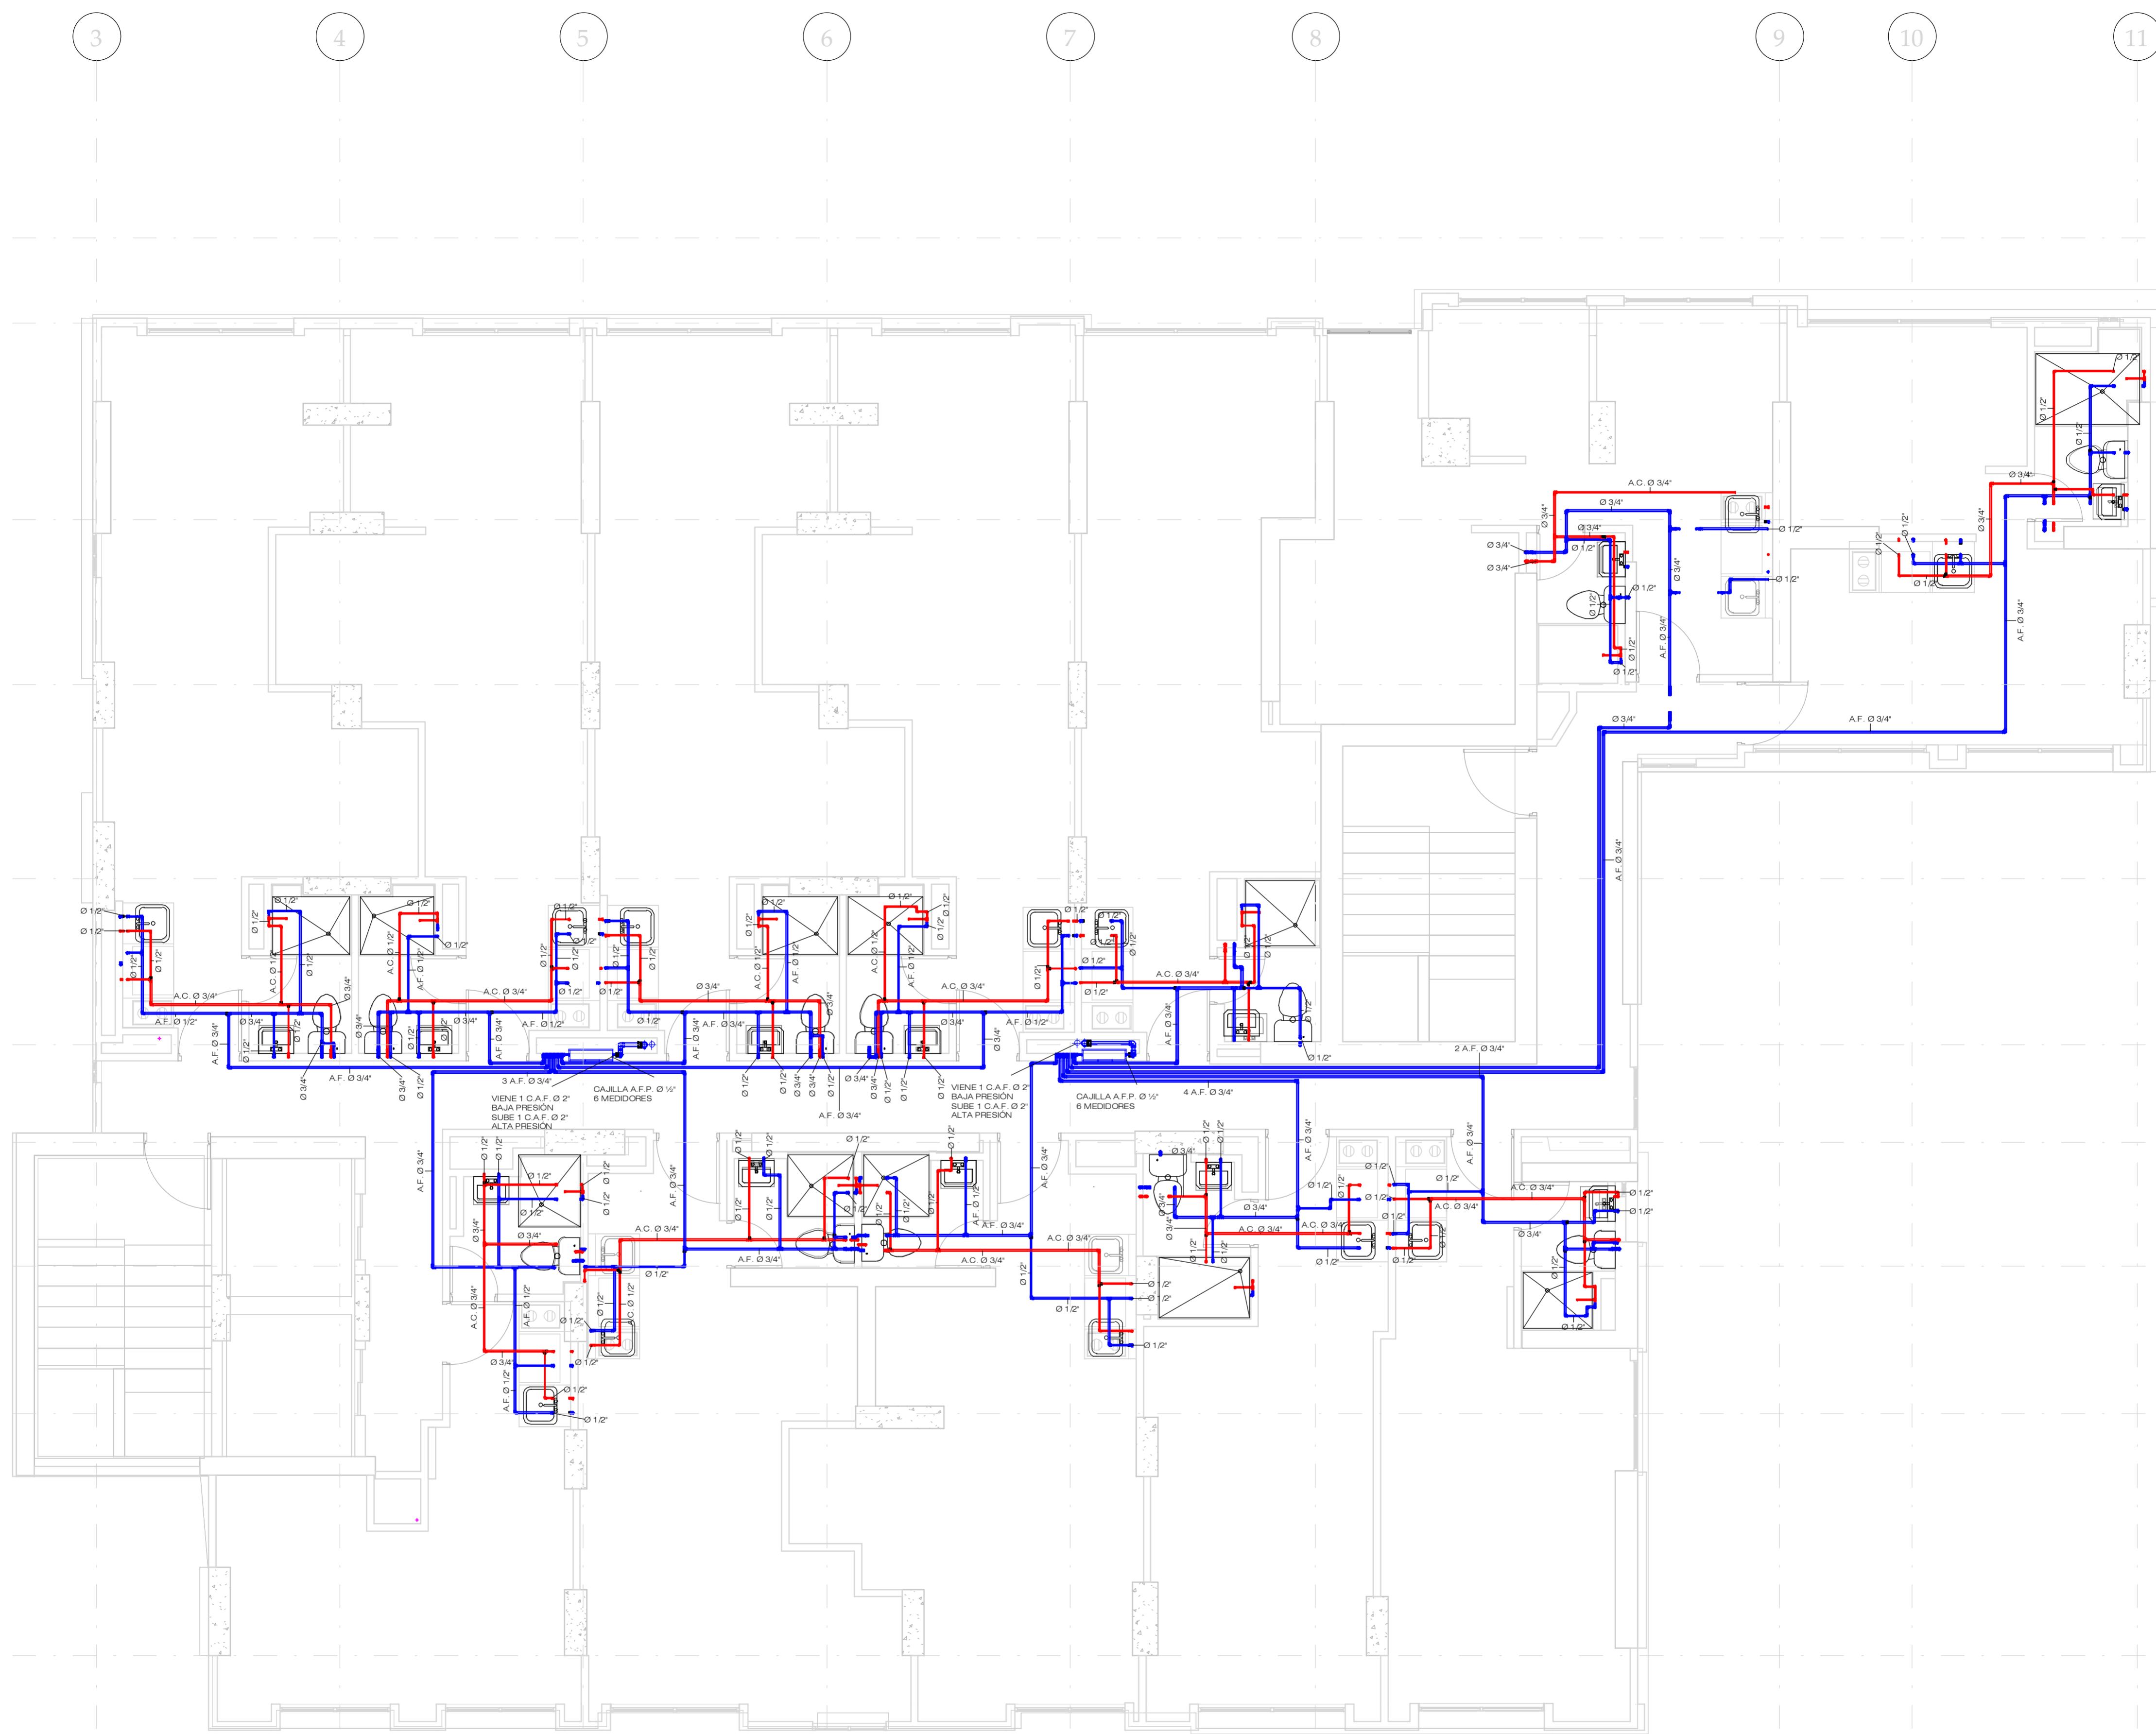


# PLANTA SUMINISTRO PISO TIPO 6-19

1 : 50



# PLANTA SUMINISTRO CUBIERTA

1 : 50

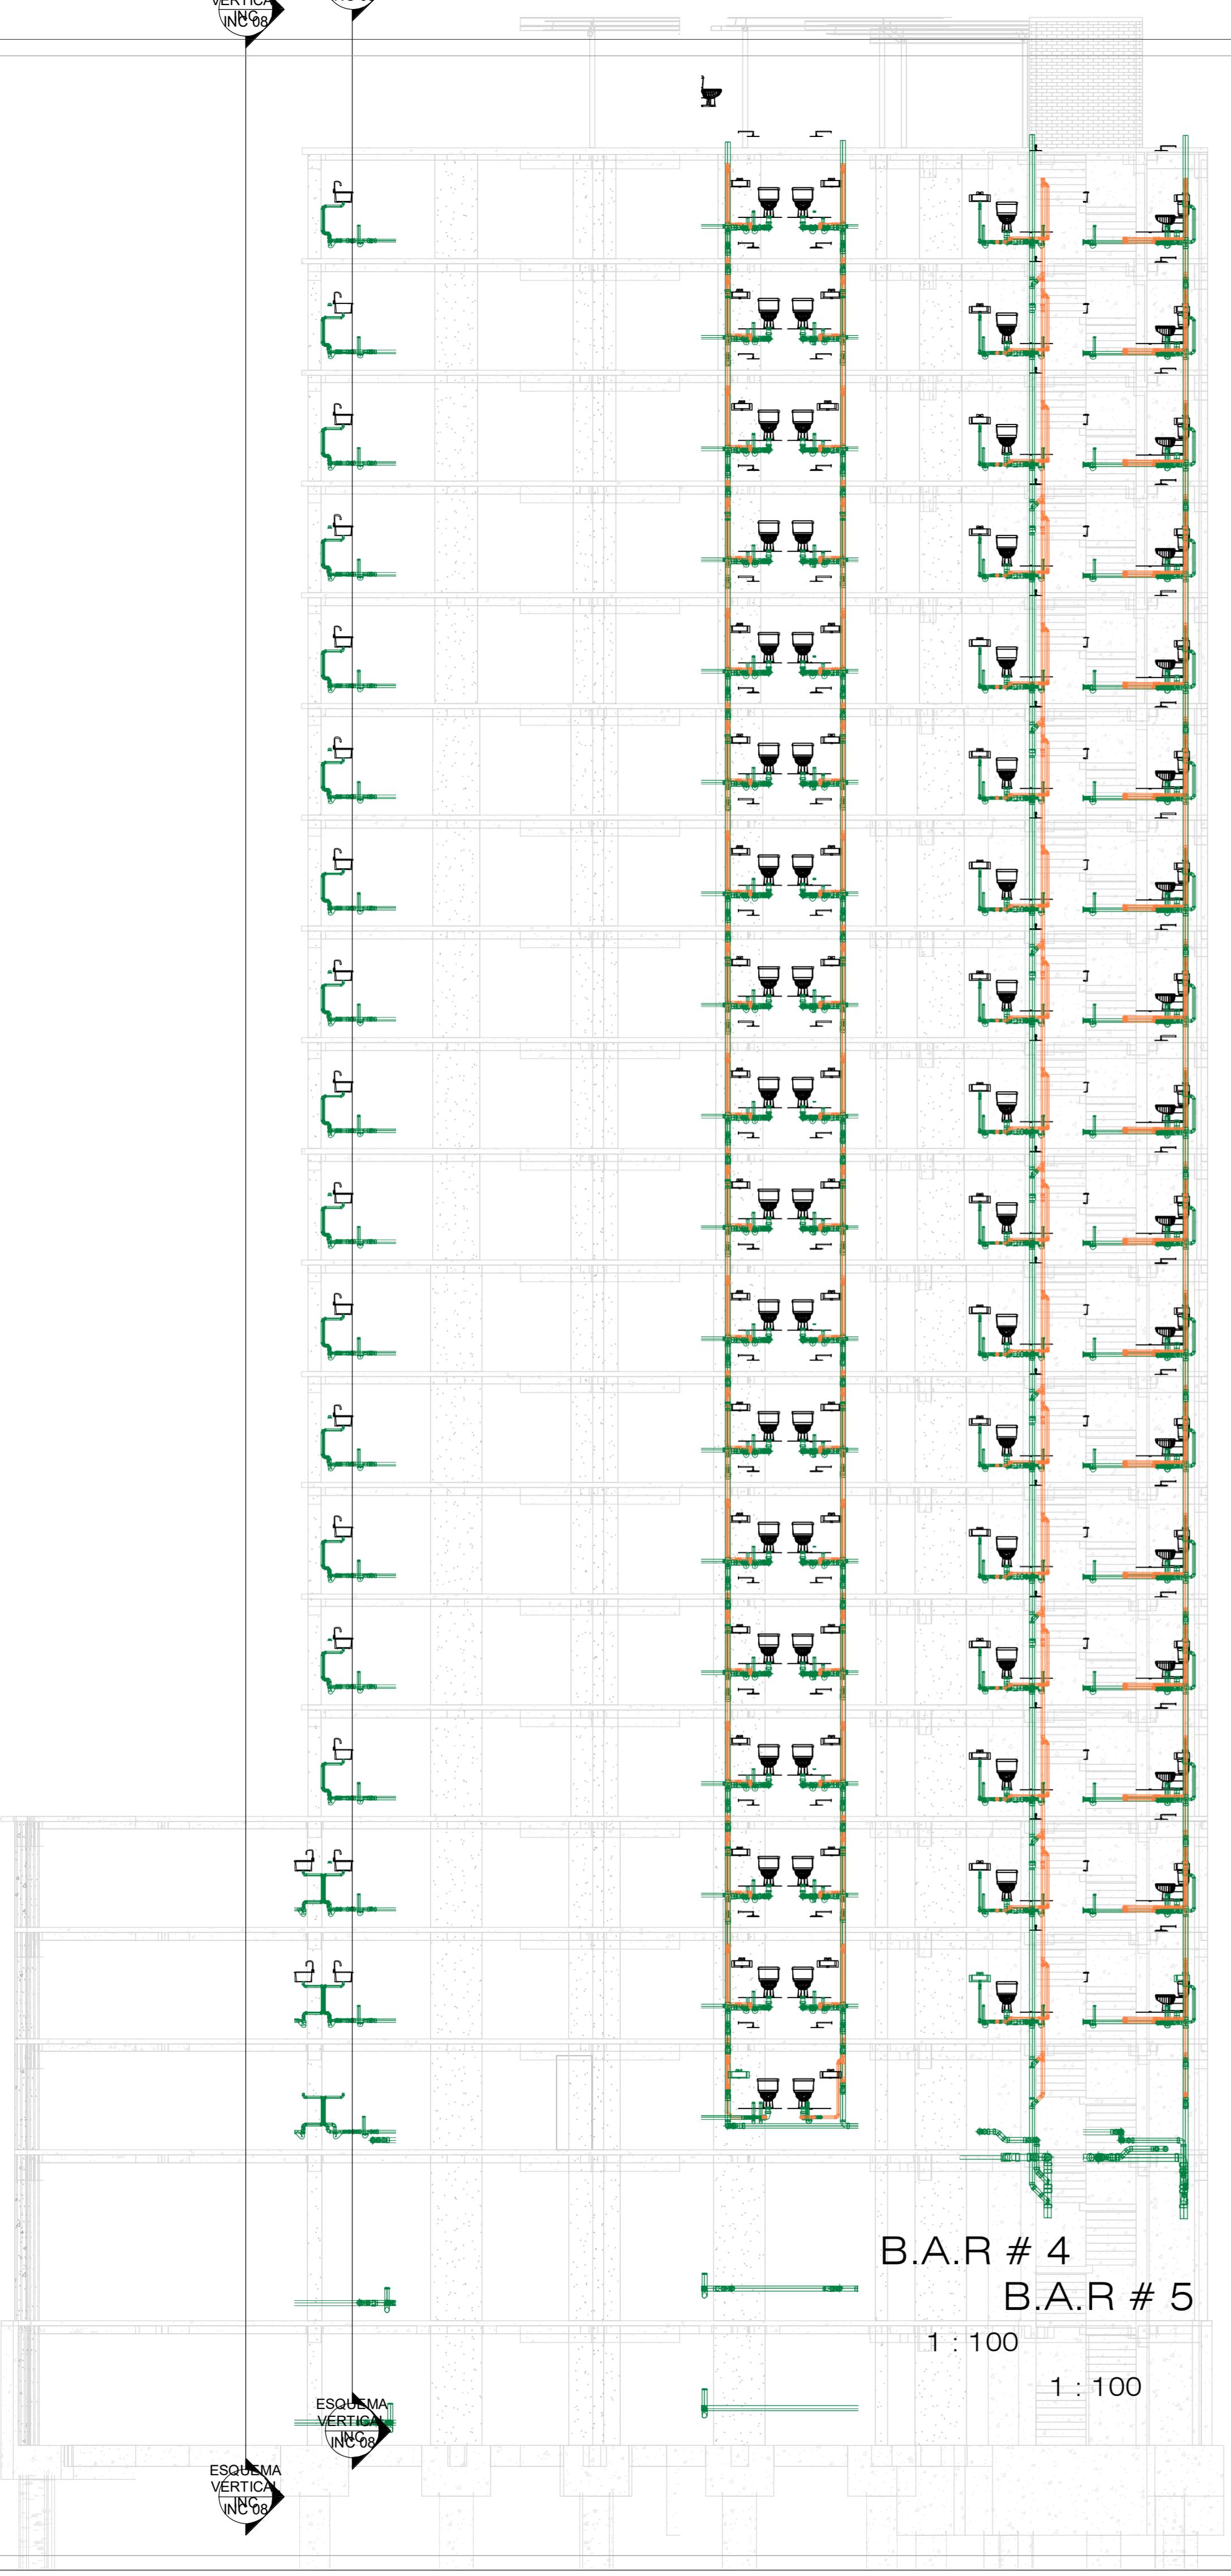

Section 2-2  
Section 3-3


B.A.R # 4


B.A.R # 5

1 : 100


1 : 100


ESQUEMA  
VERTICAL  
INC'08

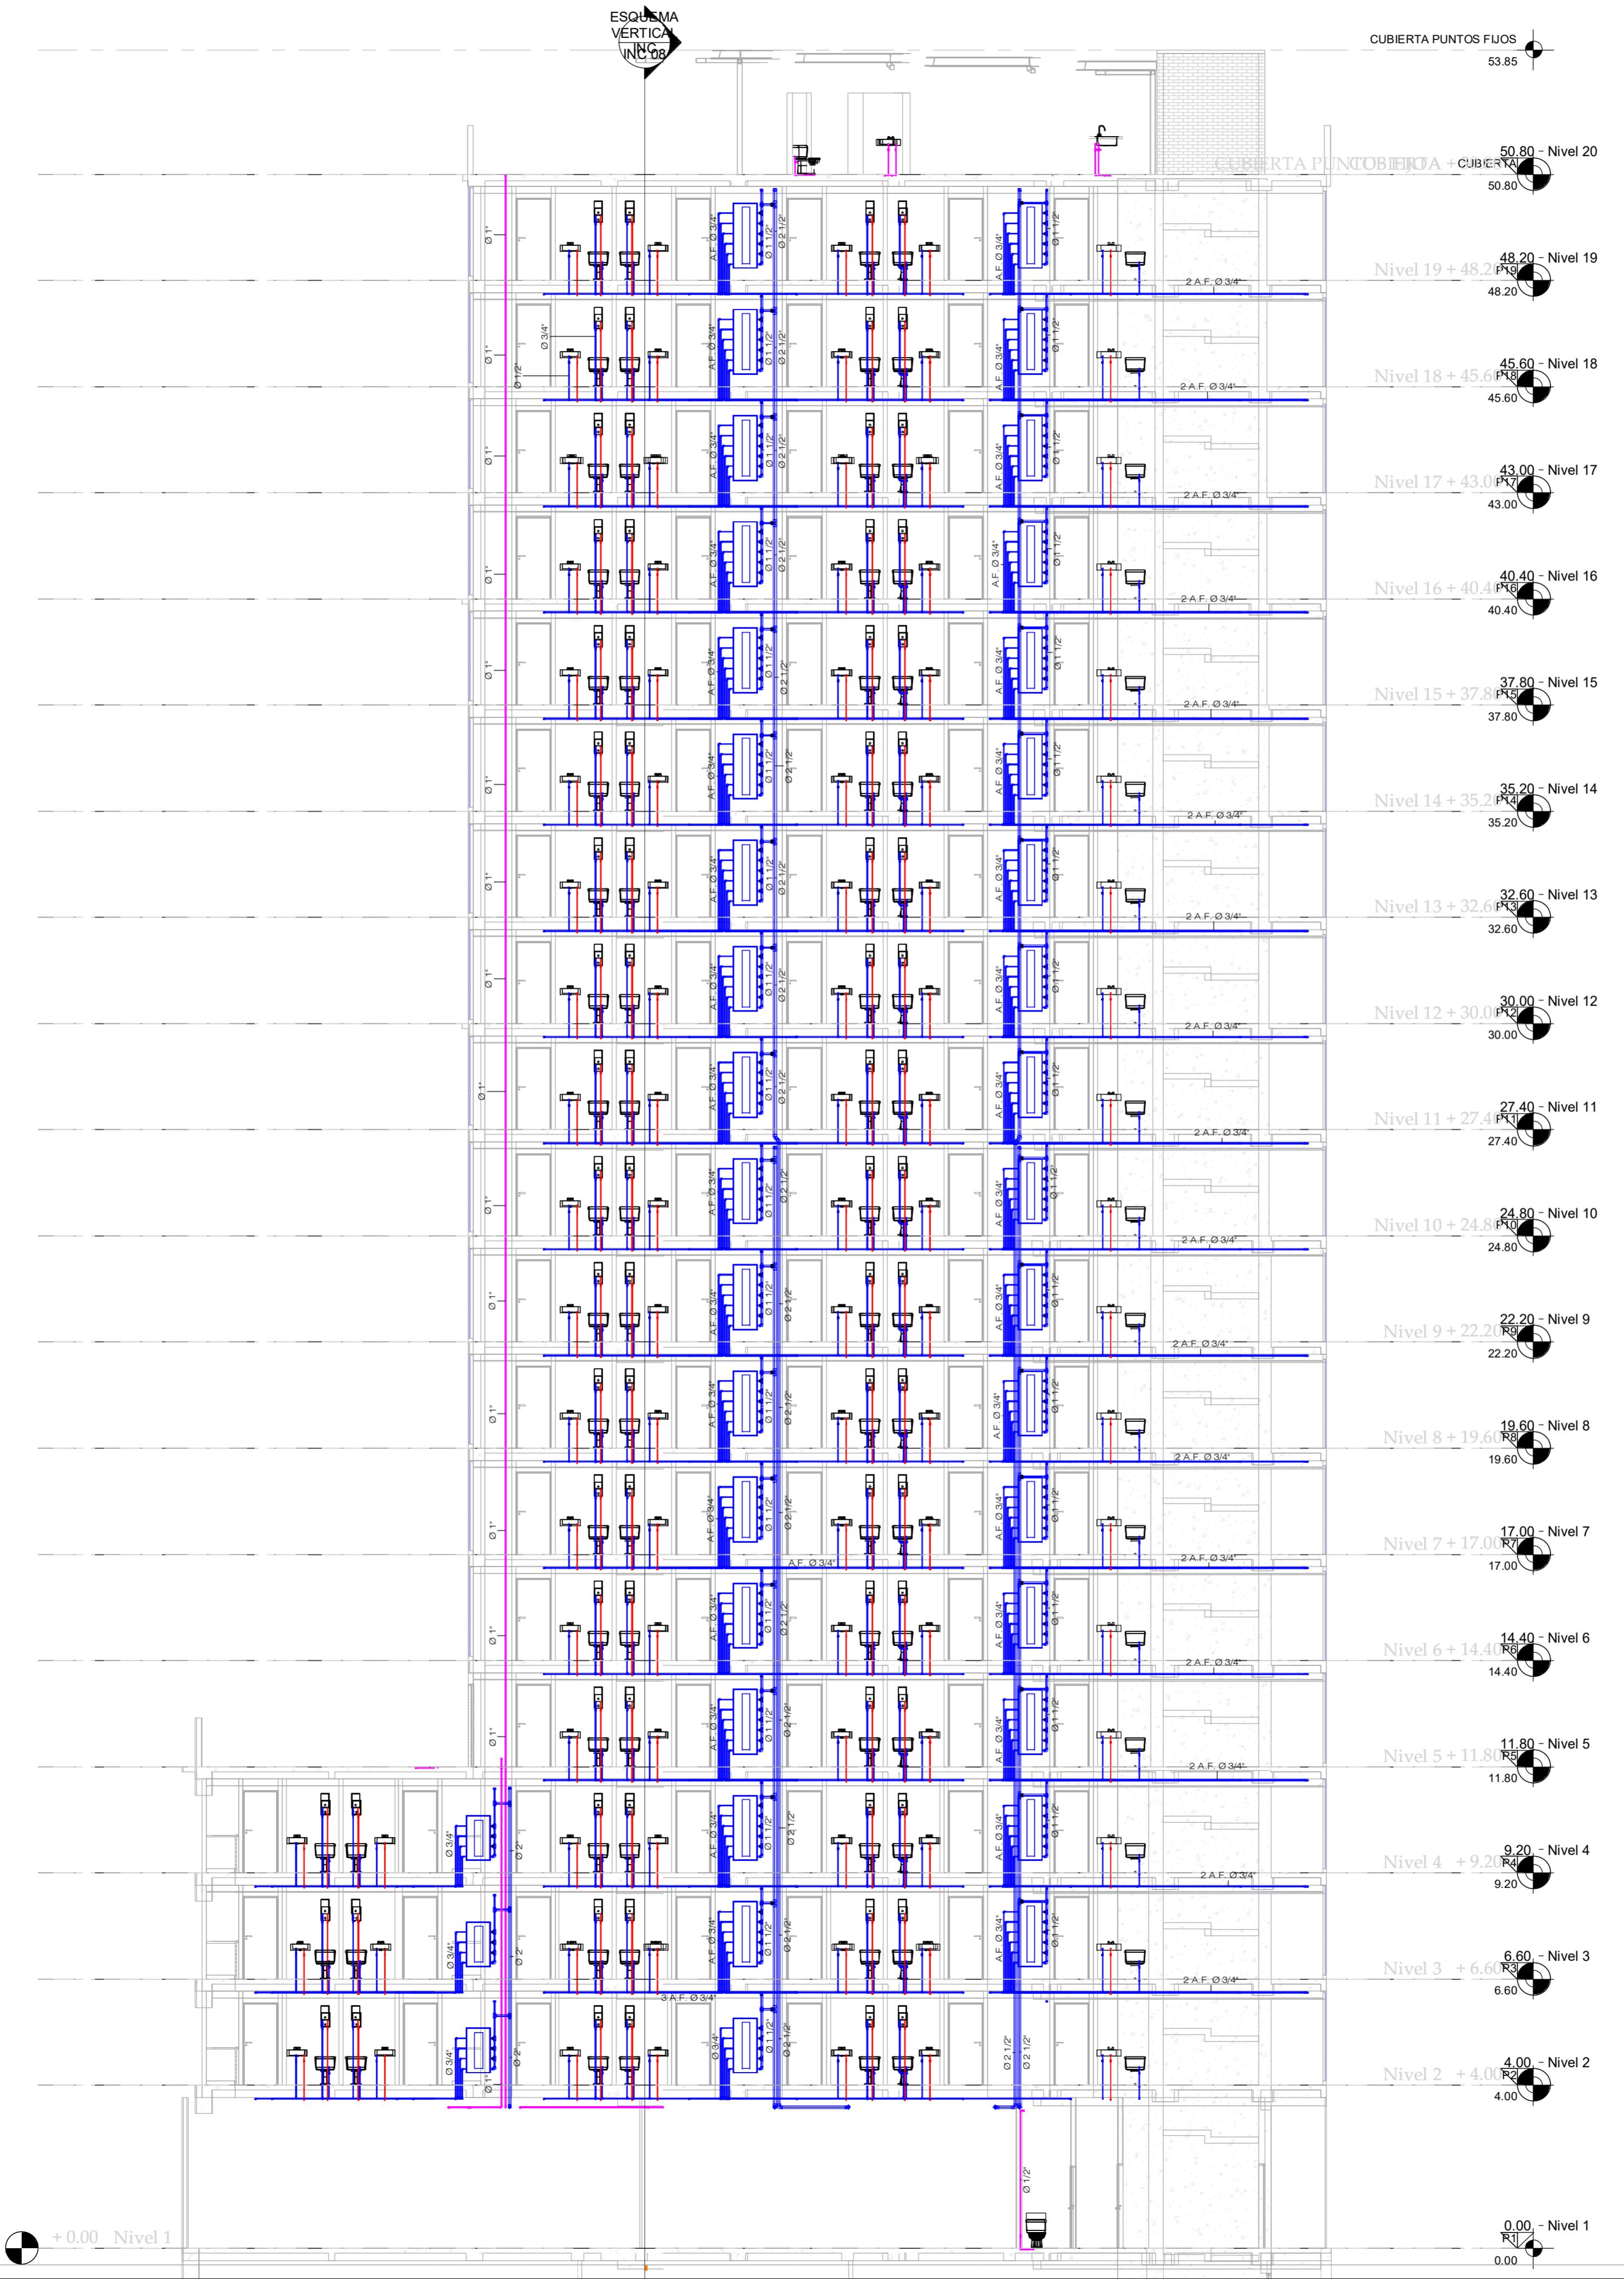

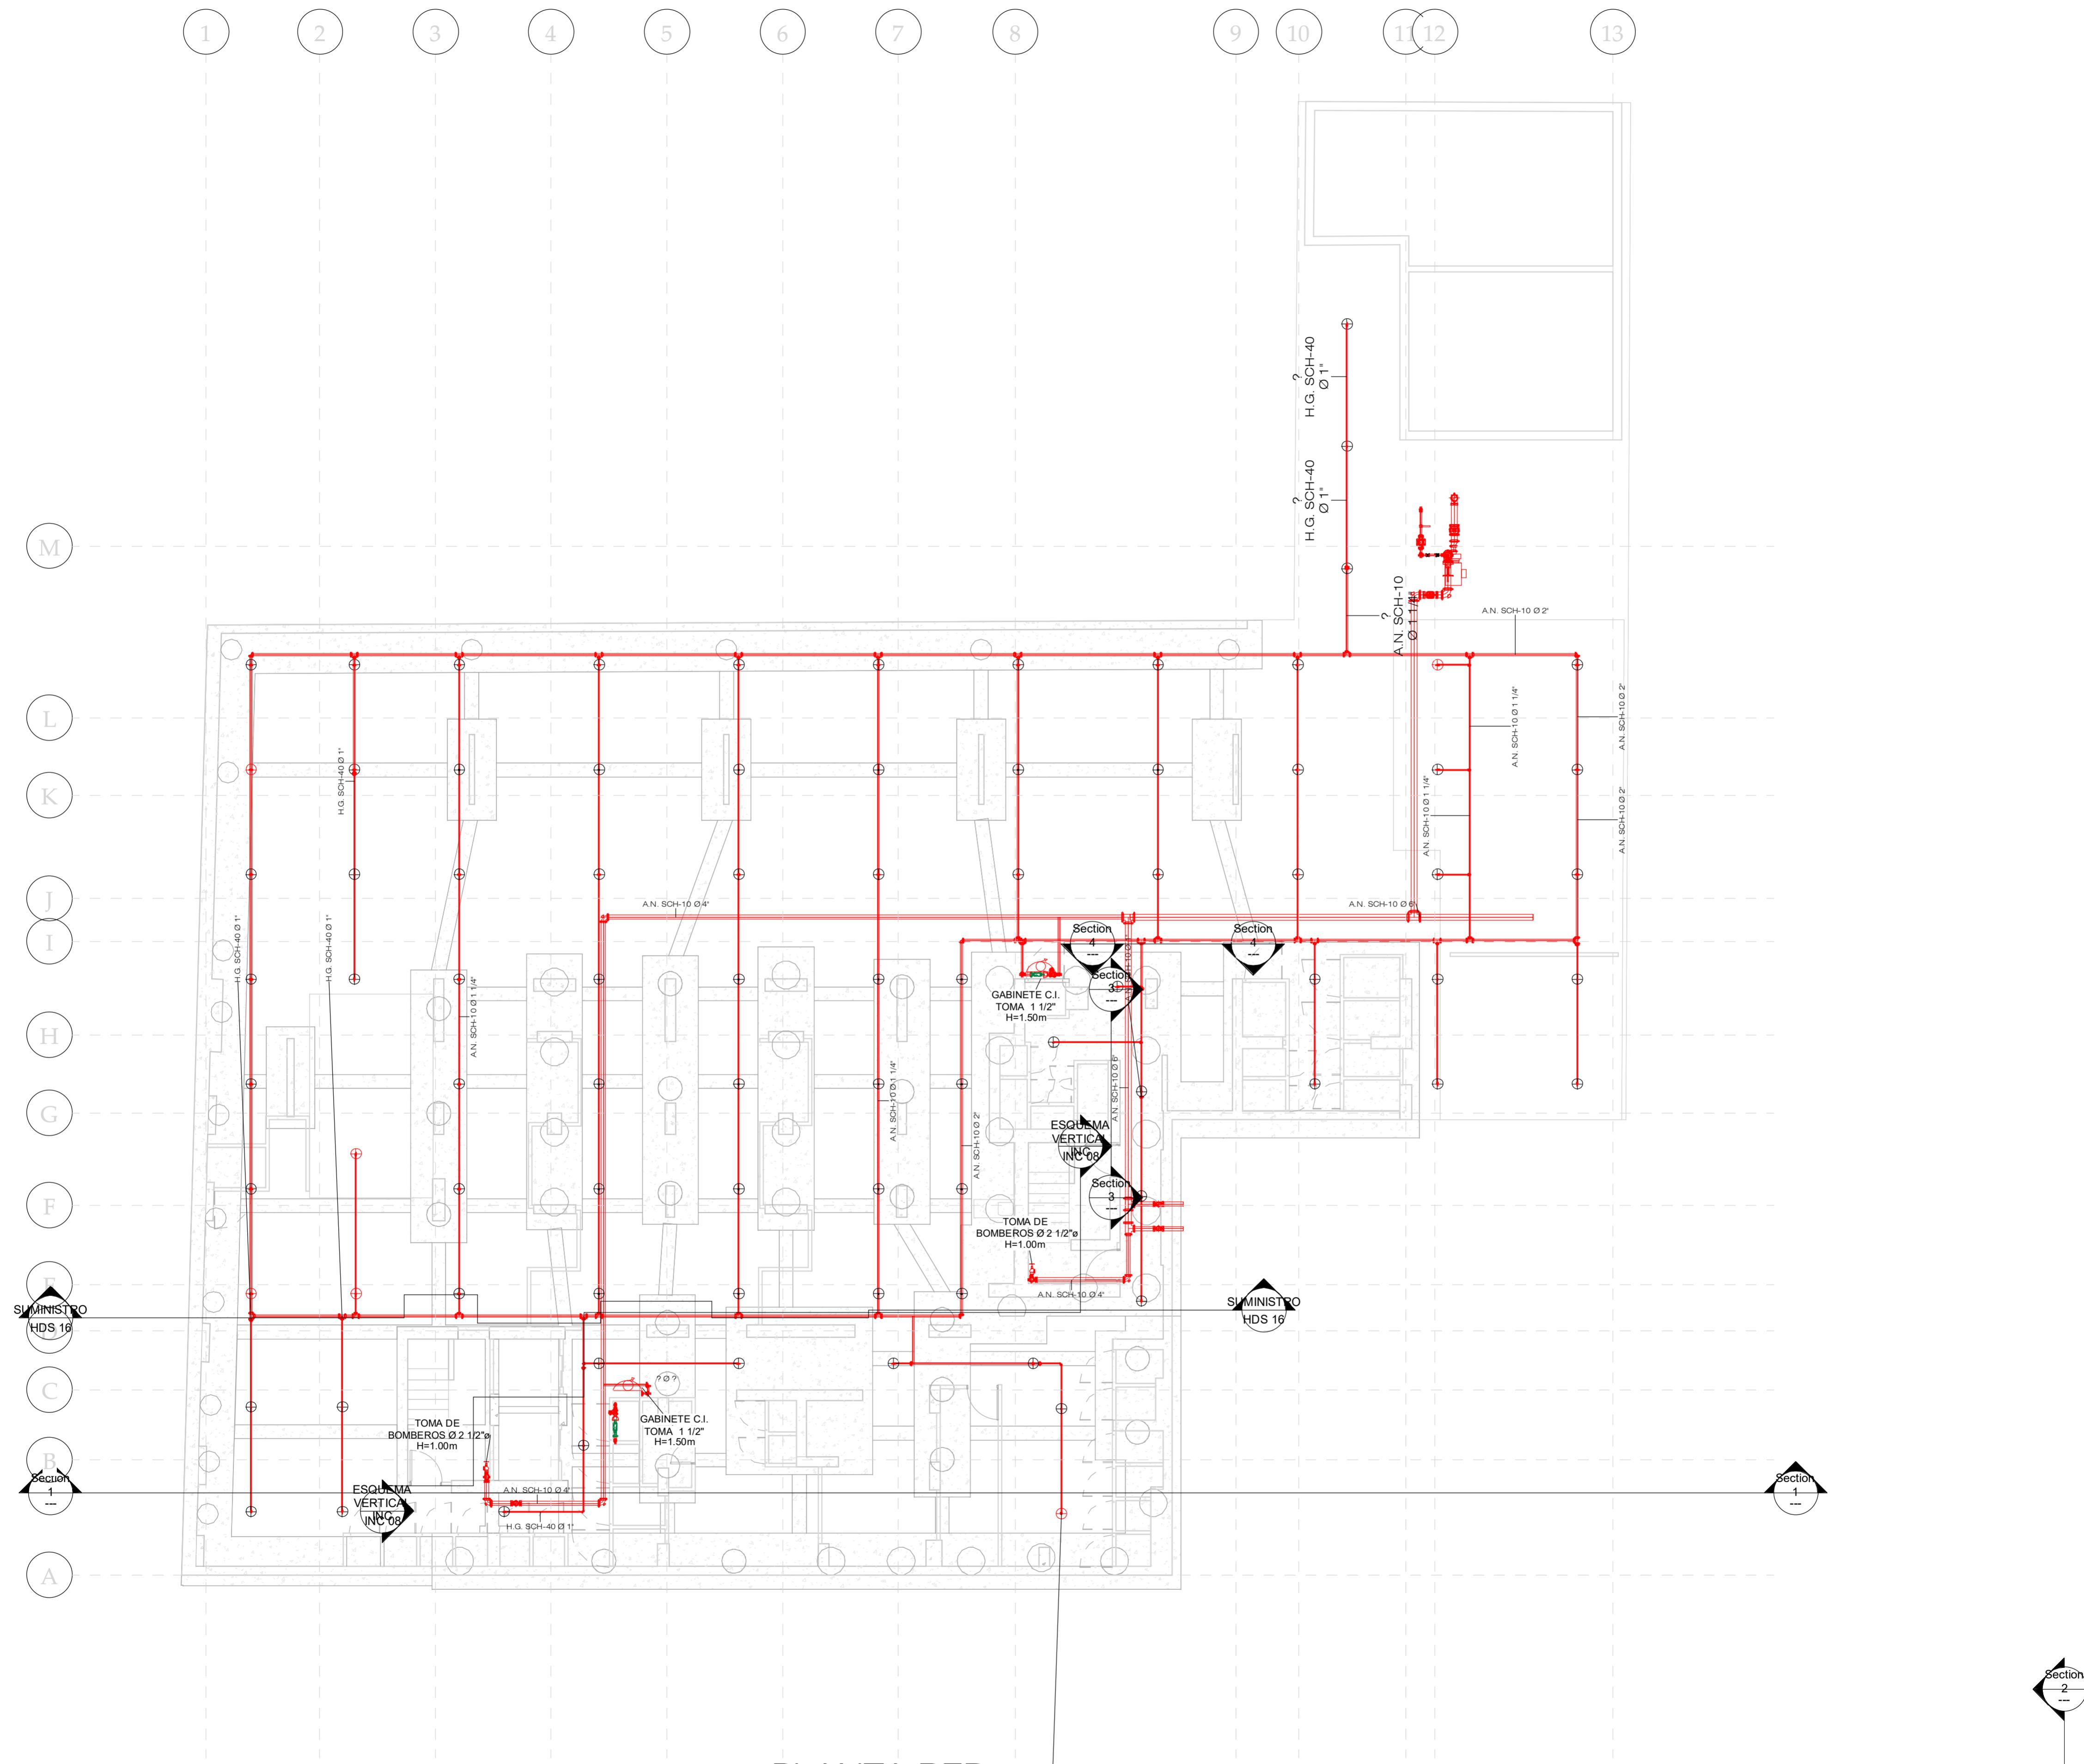


# PLANTA RED CONTRA INCENDIO SOTANO

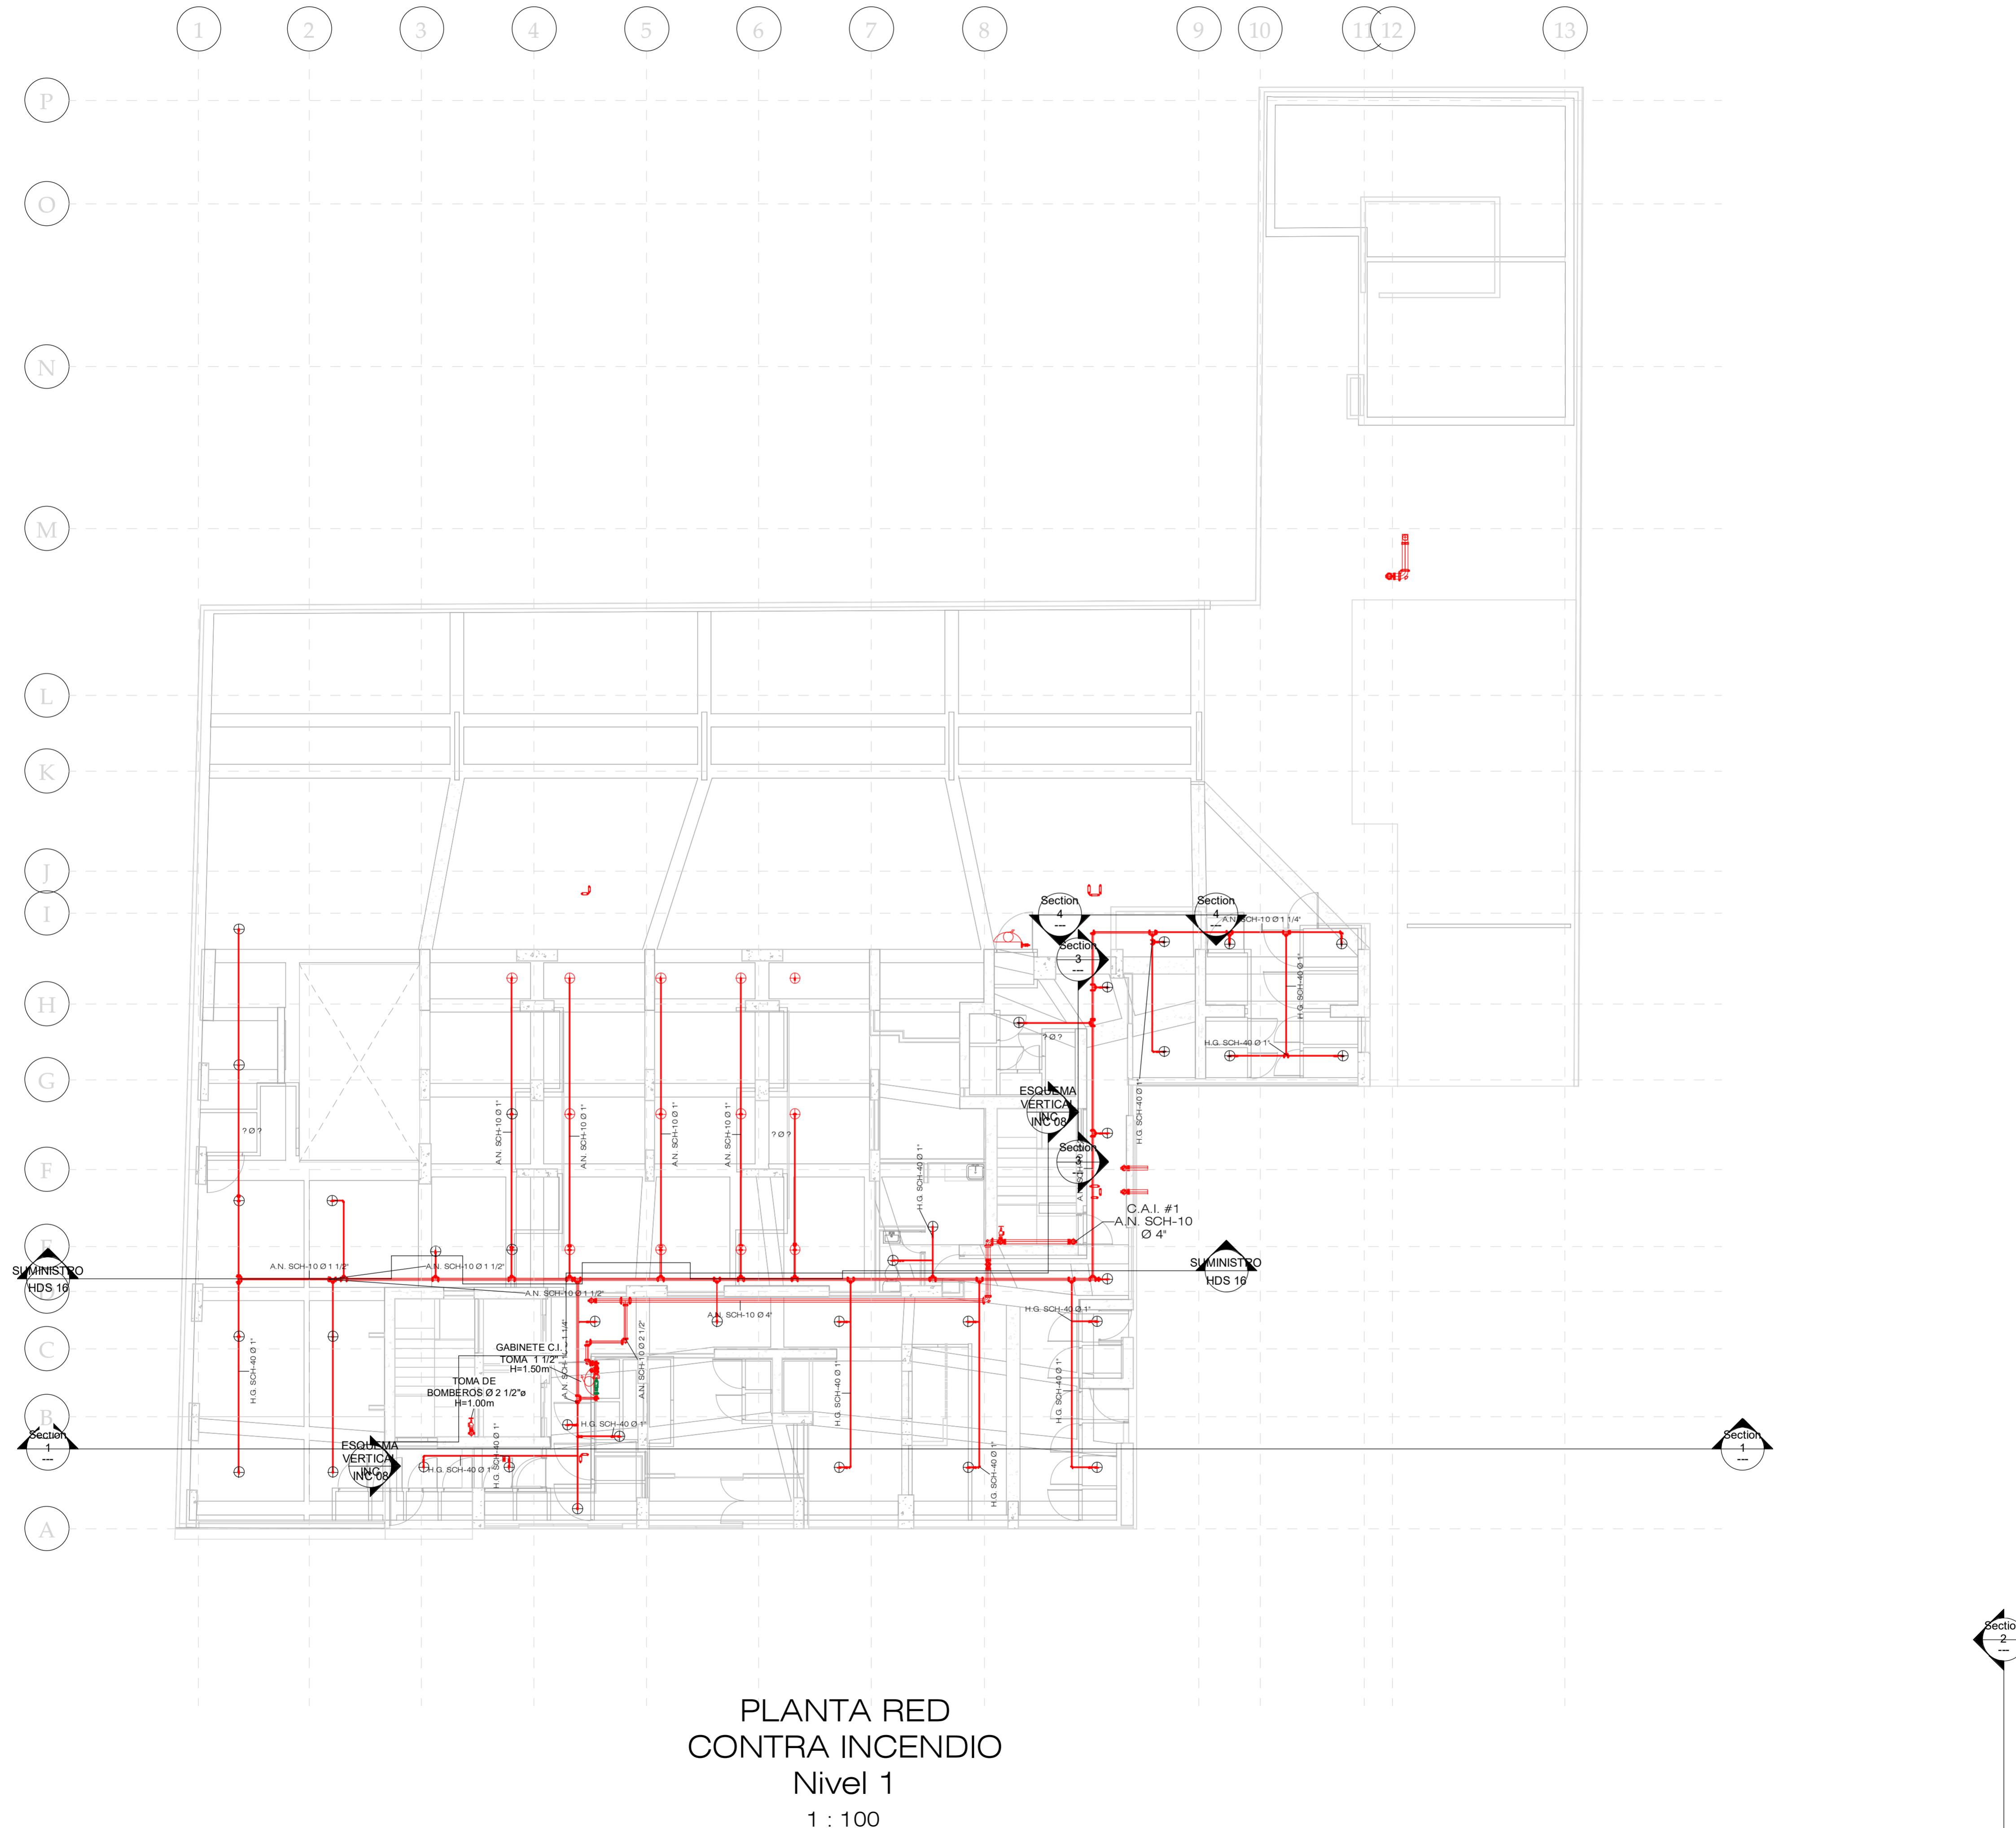

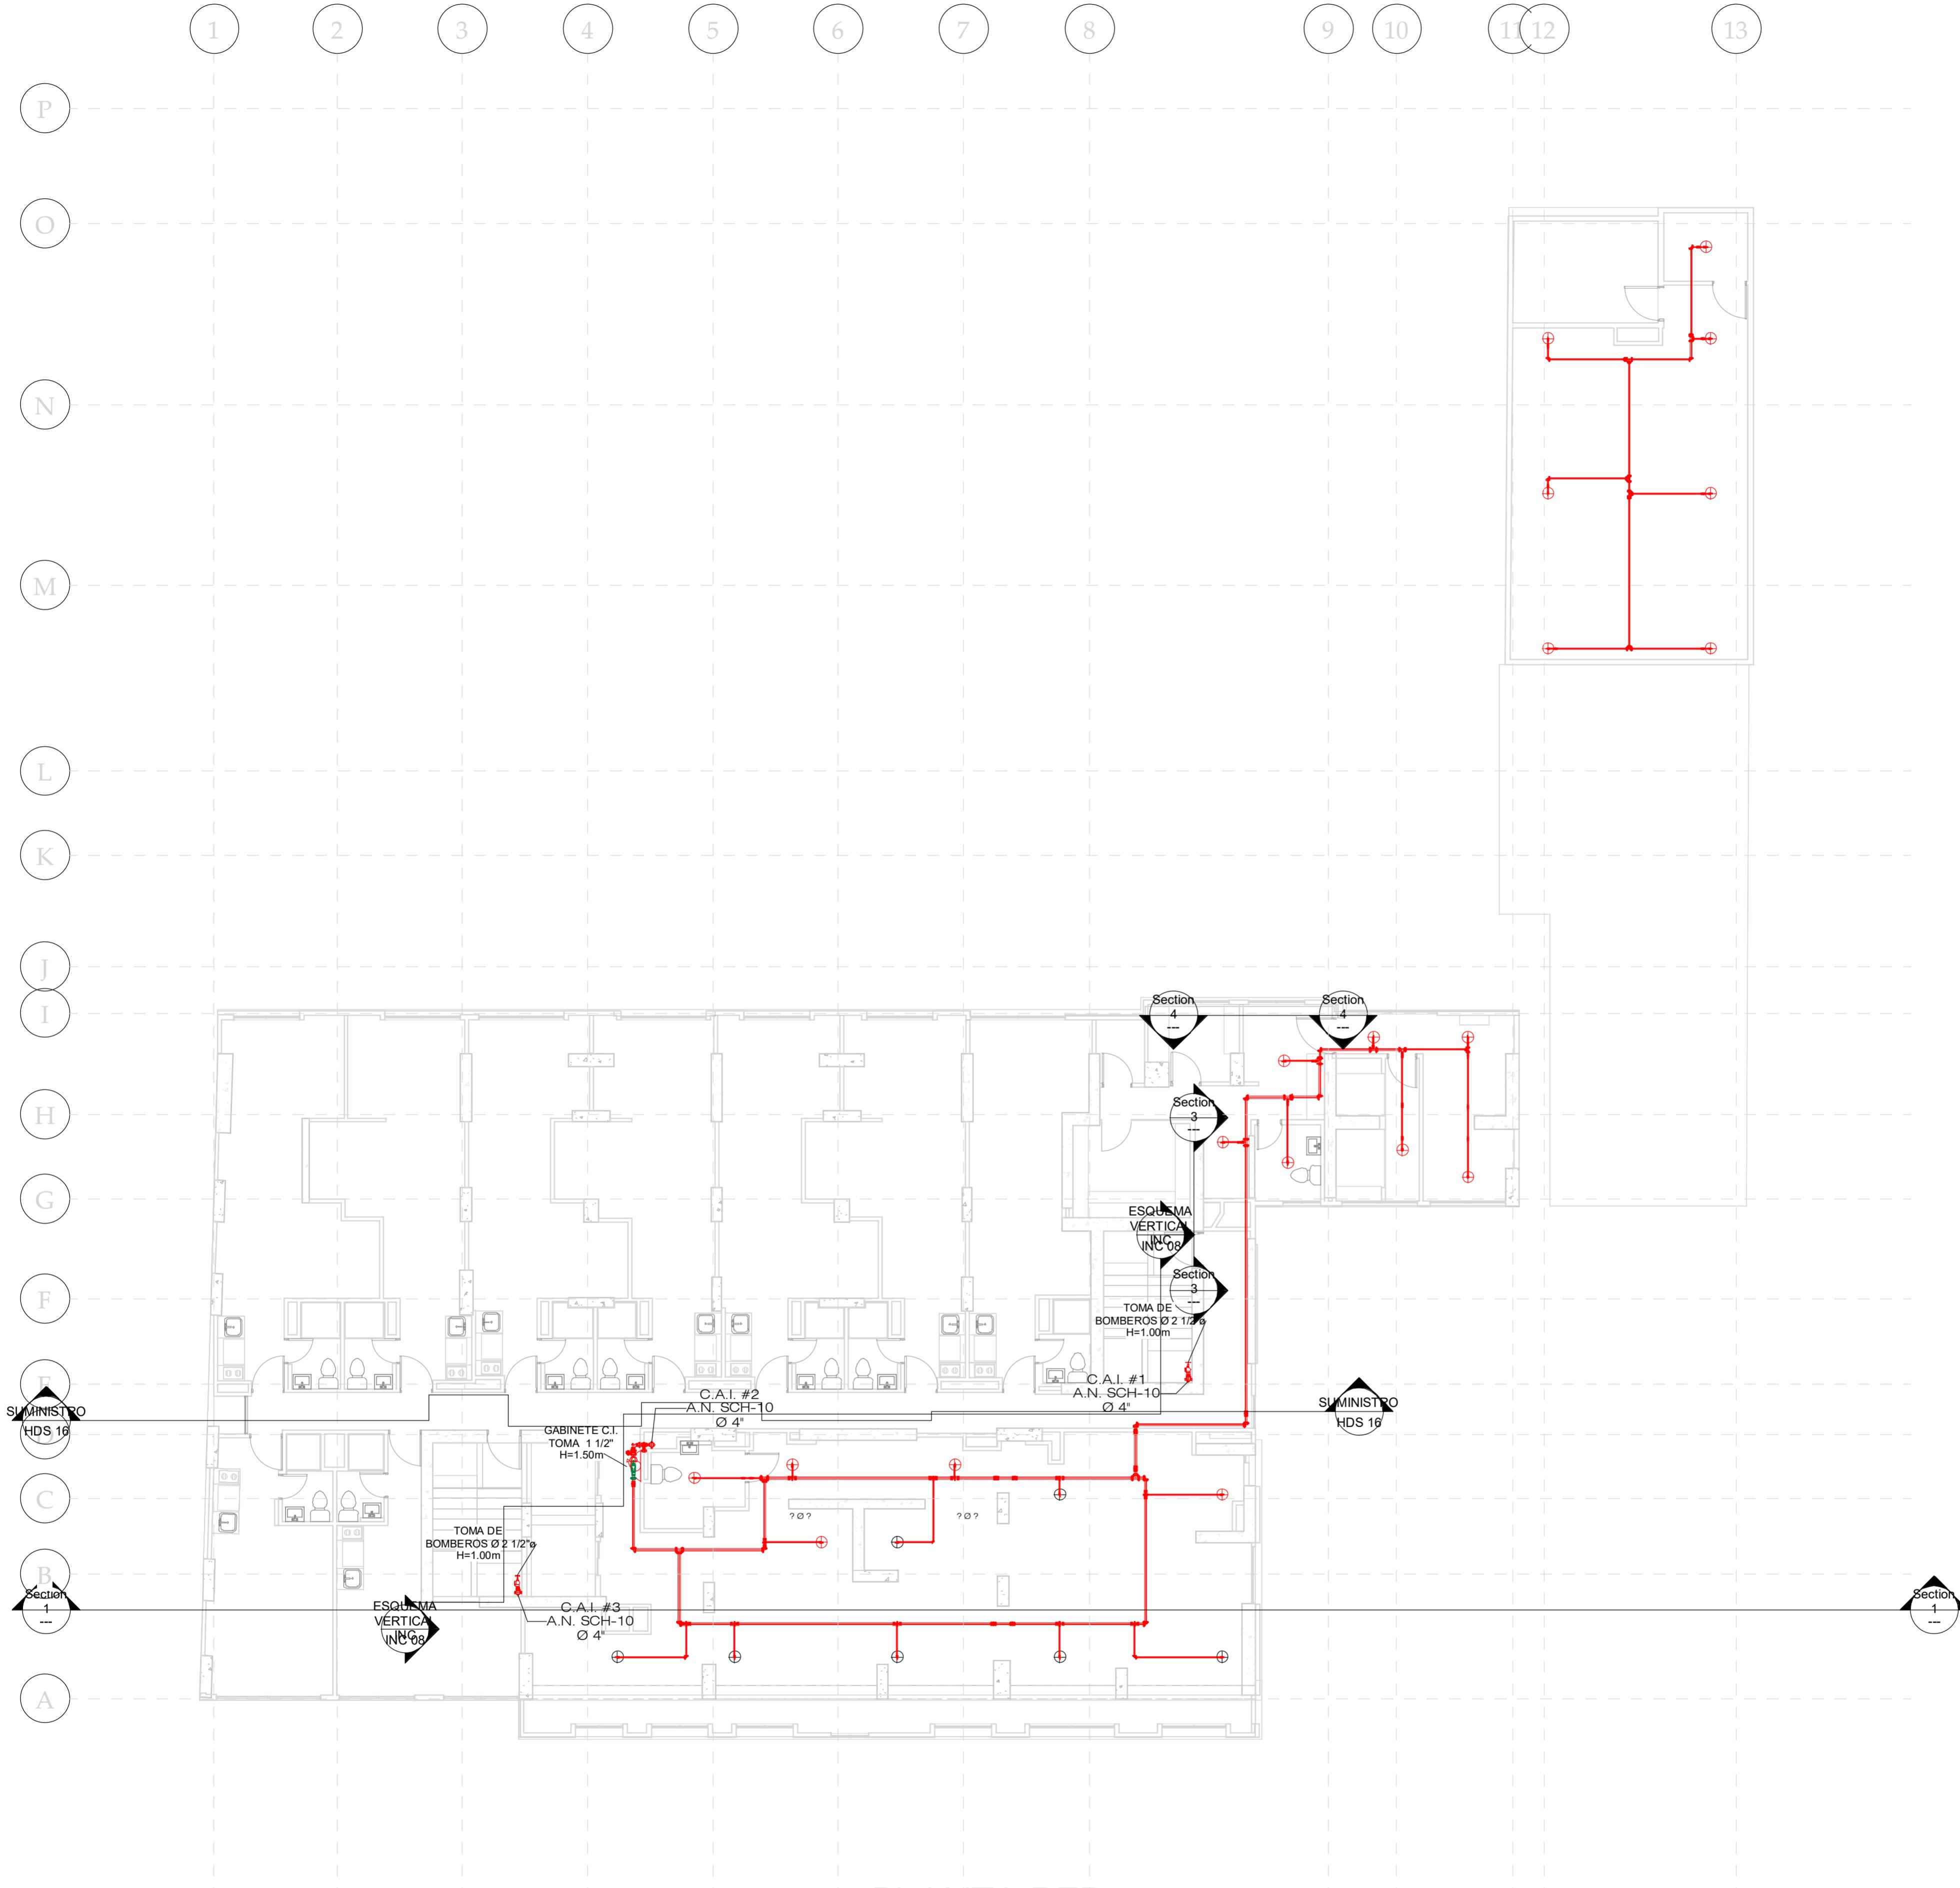

PLANTA RED  
CONTRA INCENDIO  
Nivel 2

1 : 100

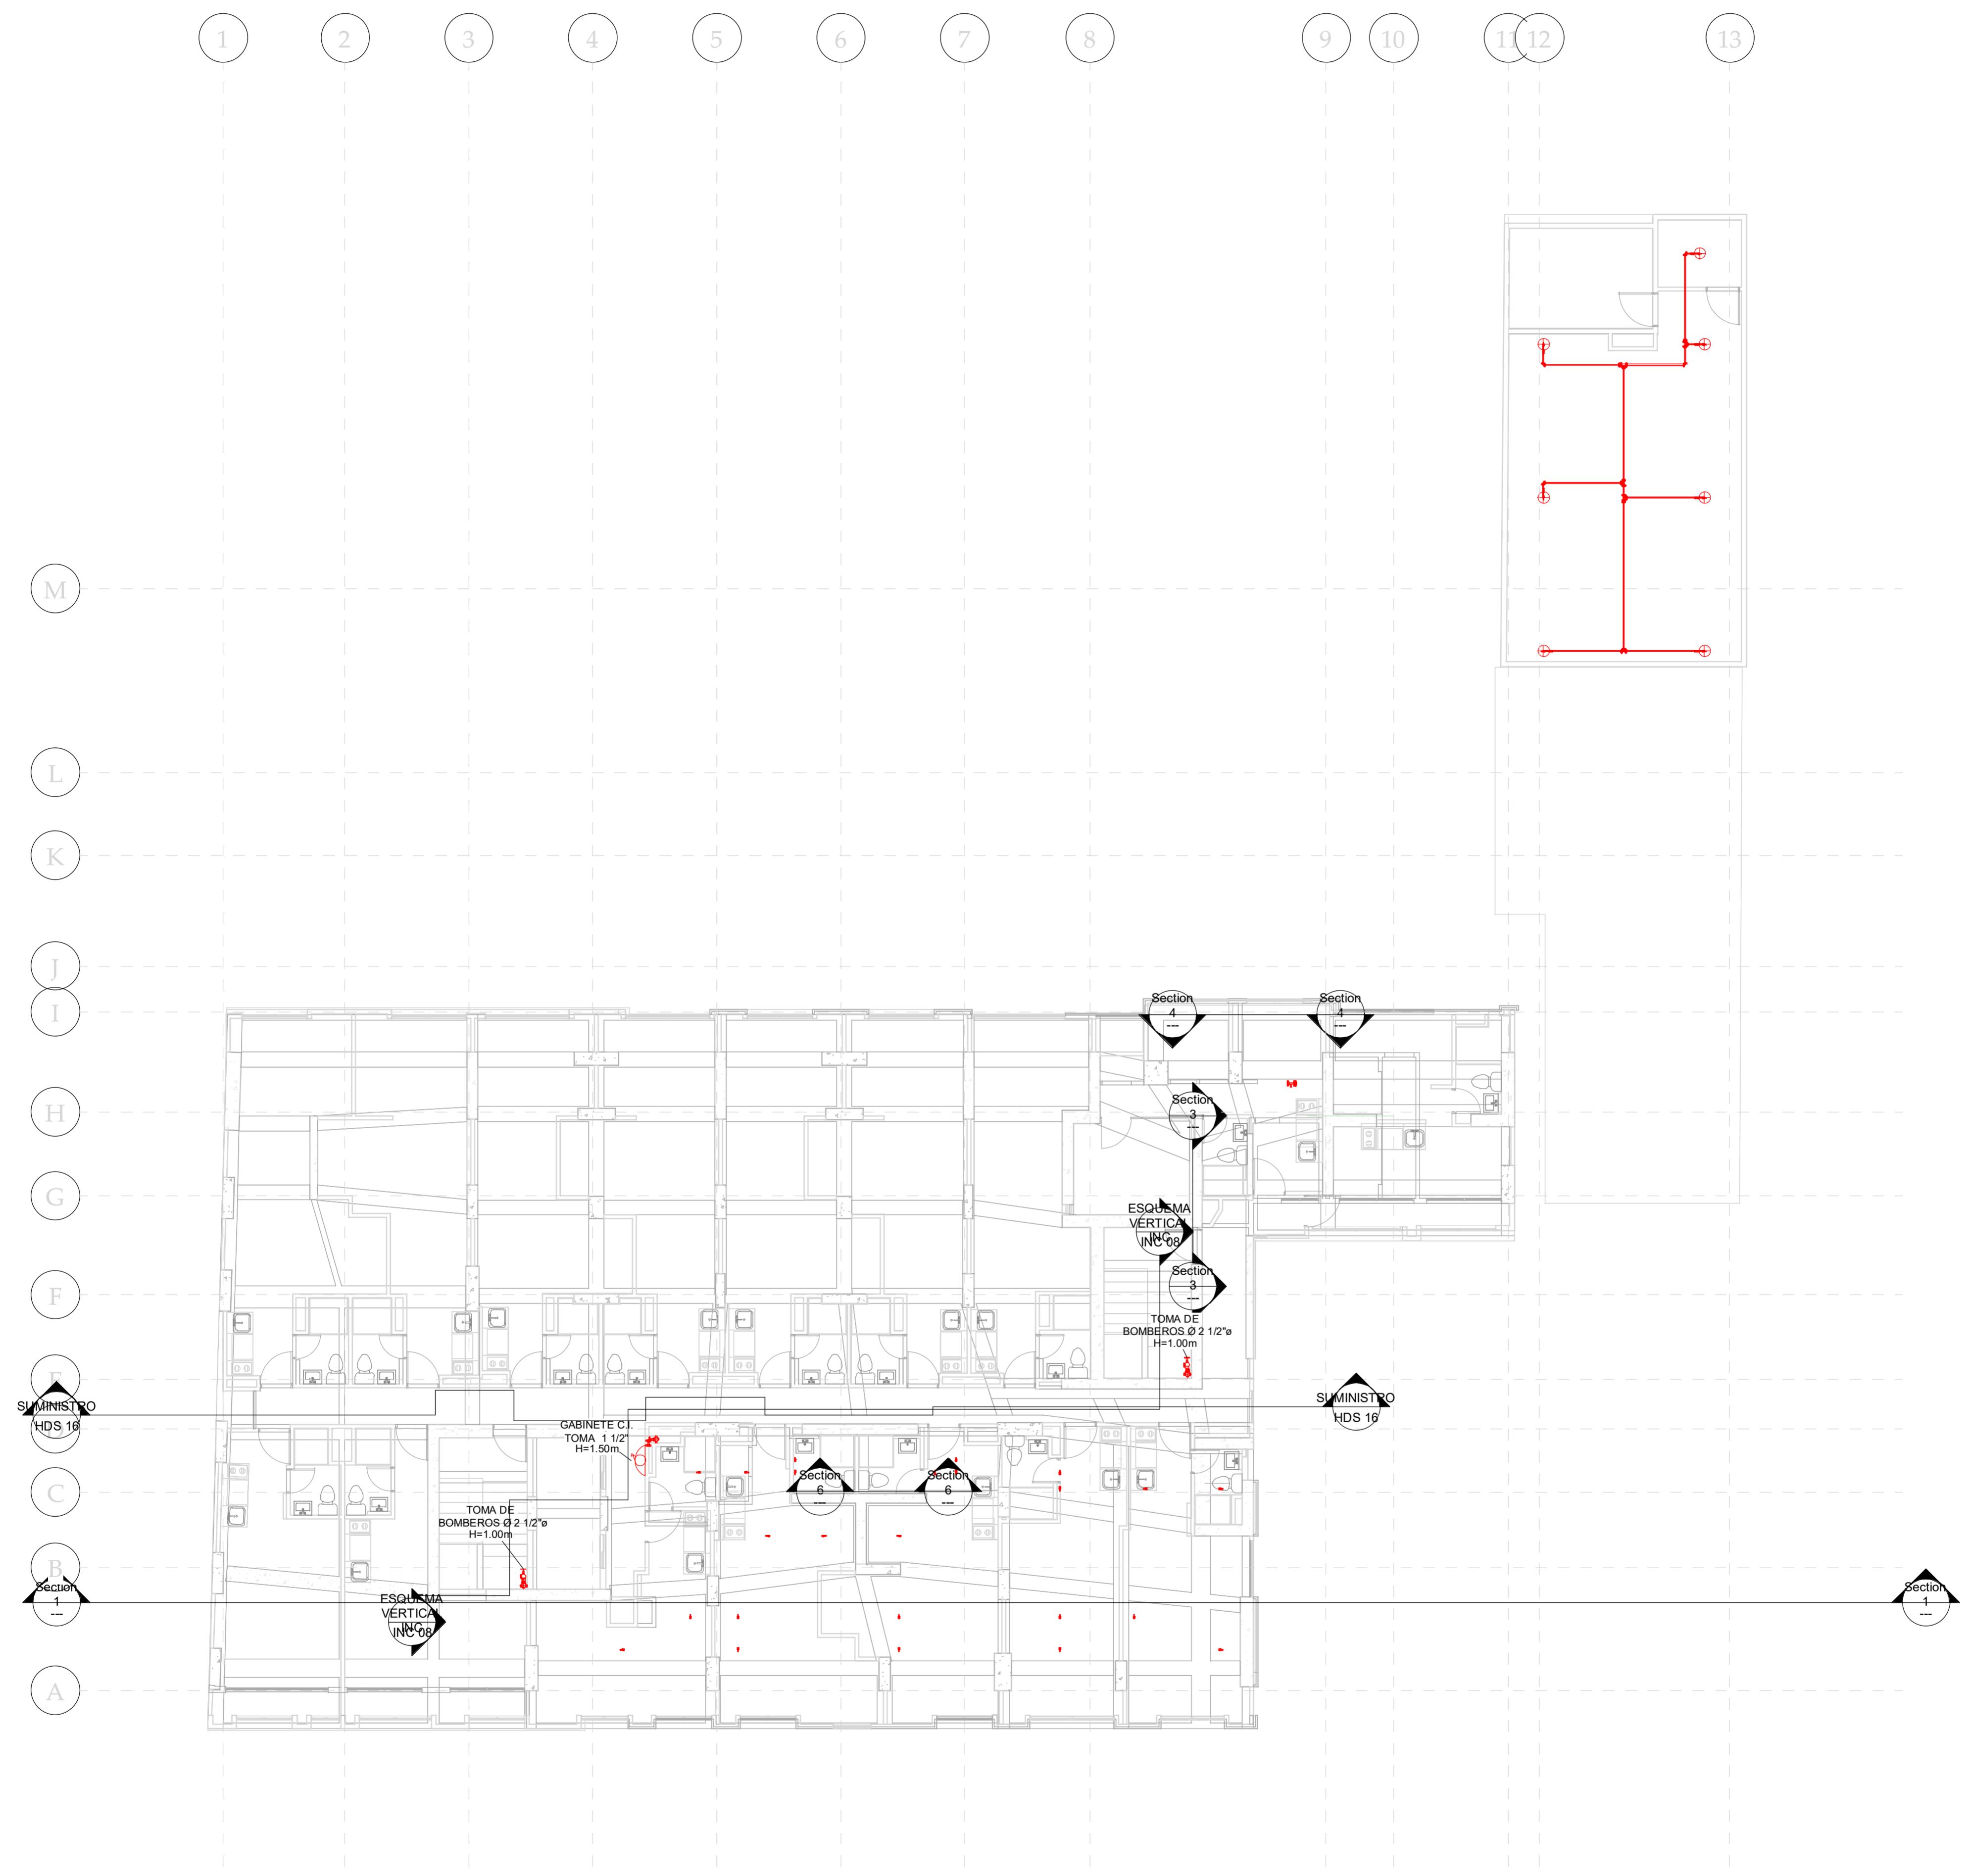


PLANTA RED  
CONTRA INCENDIO  
Nivel 3  
1 : 100



PLANTA RED  
CONTRA INCENDIO  
Nivel 5

1 : 50

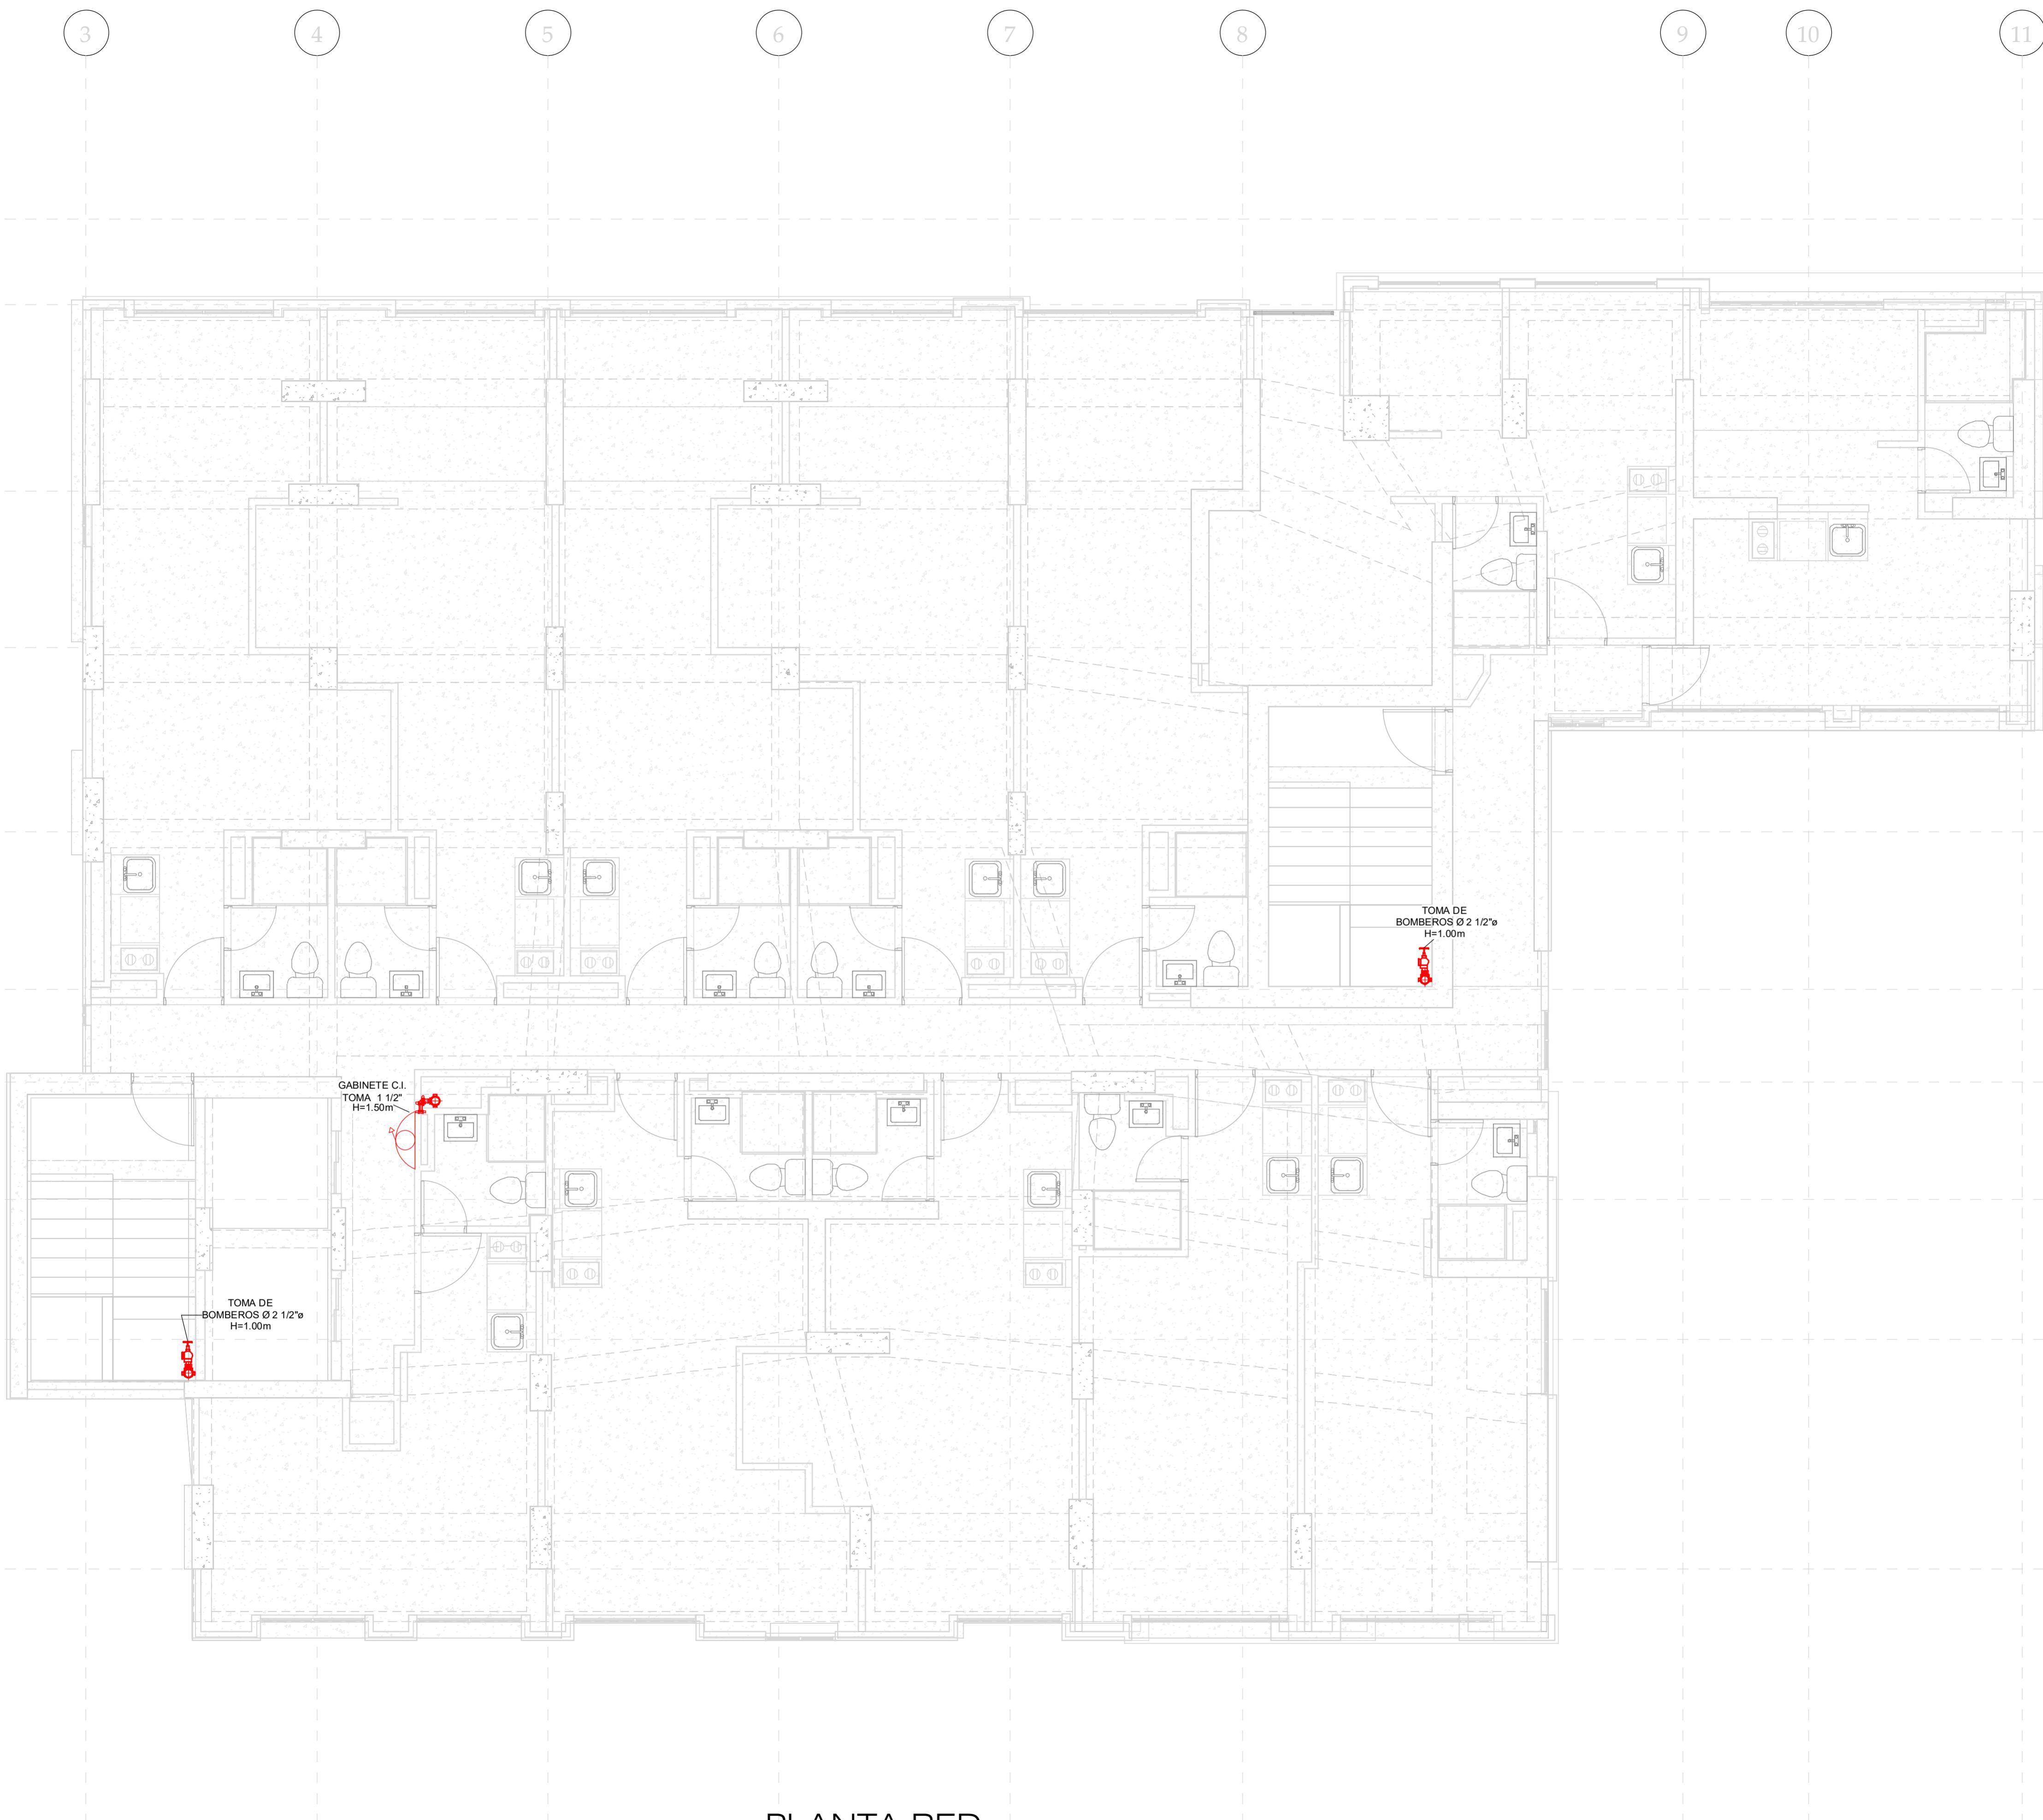

PLANTA RED  
CONTRA INCENDIO  
PISO TIPO 6-19

1 : 50



PLANTA RED  
CONTRA INCENDIO  
CUBIERTA

1 : 50

